AREAS

SITE AREA:	5312.0 m²
WAREHOUSE 1 :	387.2 m²
FIRST FLOOR OFFICE:	102.3 m²
SUB TOTAL :	489.5 m²
WAREHOUSE 2 :	179.0 m²
FIRST FLOOR OFFICE:	75.8 m²
SUB TOTAL :	254.8 m²
WAREHOUSE 3 :	227.7 m²
FIRST FLOOR OFFICE:	75.8 m²
SUB TOTAL :	303.5 m²
WAREHOUSE 4 :	227.7 m²
FIRST FLOOR OFFICE:	75.8 m²
SUB TOTAL :	303.5 m²
WAREHOUSE 5 :	179.0 m²
FIRST FLOOR OFFICE:	75.8 m²
SUB TOTAL :	254.8 m²
WAREHOUSE 6 :	254.9 m²
FIRST FLOOR OFFICE:	95.7 m²
SUB TOTAL :	350.6 m²
WAREHOUSE 7 :	254.9 m²
FIRST FLOOR OFFICE:	95.7 m²
SUB TOTAL :	350.6 m²
WAREHOUSE 8 :	179.0 m²
FIRST FLOOR OFFICE:	75.8 m²
SUB TOTAL :	254.8 m²
WAREHOUSE 9 :	227.7 m²
FIRST FLOOR OFFICE:	75.8 m²
SUB TOTAL :	303.5 m²
WAREHOUSE 10 :	227.7 m²
FIRST FLOOR OFFICE:	75.8 m²
SUB TOTAL :	303.5 m²
WAREHOUSE 11 :	179.0 m²
FIRST FLOOR OFFICE:	75.8 m²
SUB TOTAL :	254.8 m²
WAREHOUSE 12 :	387.2 m²
FIRST FLOOR OFFICE:	102.3 m²
SUB TOTAL :	489.5 m²
TOTAL AREA:	3913.4 m²
SITE COVERAGE:	73.6 %

TOTAL CARPARKS: 62 OFF

- ALL CARPARKS TO BE 2600W x 4900L MIN
- CARPARKS FOR DISABLED TO BE 2 No 2400 x 5400 LONG MIN
- ALL LOADING BAYS TO BE 3600W & 4500 x 4300H x 7600L MIN

NOTE:
ALL 62 CAR SPACES TO BE LINE - MARKED AND UTILIZED UPON COMPLETION OF THE PERMITTED DEVELOPMENT

CARPARK SHORTFALL: 2 OFF

LEGEND:

BF — 1 No BICYCLE FACILITY RACK 1700 x 700 x 1200 HIGH PROVIDE SIGNAGE 300 x 450 HIGH (TYP) WITH BICYCLE LOCKER STORAGE

BICYCLE FACILITY SPACE

RH — ROOF HATCH

RWT — 2500 LITRE RAINWATER TANK


LEGEND:

1540 / 1450 / MAP — DENOTES ACCESS PATH FOR ACCESS FOR DISABLED AT ENTRY TO BUILDING

AS — SIGNAGE FOR ACCESS DOOR TO BUILDING SHALL BE PROVIDED WITH THE LETTERS ACCESS TO ADVISE THE ENTRY TO THE BUILDING FOR DISABLED PERSONS . THE MINIMUM FONT SIZE SHALL BE 20mm SAN SERIF. SUCH SIGN SHALL BE IDENTIFIED BY THE USE OF ENGLISH WORDS AND LOCATED BETWEEN 1200mm - 1600mm ABOVE FINISHED FLOOR LEVEL.




ACCESS SIGNAGE FOR DISABLED LOCATED AT EXTERNALLY AT ENTRY DOOR

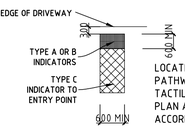

LOCATION OF TACTILE INDICATOR AT EDGE OF PATHWAY LEADING TO CARPARK AREAS. ALL TACTILE INDICATORS AS SHOWN ON SITE PLAN ARE TO BE PLACED AND INSTALLED IN ACCORDANCE WITH AS 1428.4 -2009

TACTILE INDICATORS AT ENTRY POINTS

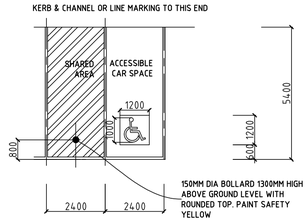

ACCESSIBLE CAR PARKING SPACES IN ACCORDANCE WITH AS 2890.6

SPACE IDENTIFICATION

EACH DEDICATED SPACE SHALL BE IDENTIFIED BY MEANS OF A WHITE SYMBOL OF ACCESS IN ACCORDANCE WITH AS 1428.1 BETWEEN 800 MM AND 1000 MM HIGH PLACED ON A BLUE RECTANGLE WITH NO SIDE MORE THAN 1200 MM, PLACED AS A PAVEMENT MARKING IN THE CENTRE OF THE SPACE BETWEEN 500 MM AND 600 MM FROM ITS ENTRY POINT AS ILLUSTRATED


SPACE DELINEATION

PAVEMENT MARKINGS SPECIFIED IN ITEMS (A) AND (B) OF THIS CLAUSE SHALL BE YELLOW AND SHALL HAVE A SLIP RESISTANT SURFACE. RAISED PAVEMENT MARKERS SHALL NOT BE USED FOR SPACE DELINEATION.

PAVEMENT MARKINGS SHALL BE PROVIDED AS FOLLOWS:

1. DEDICATED PARKING SPACES SHALL BE OUTLINED WITH UNBROKEN LINES 80 TO 100 MM WIDE ON ALL SIDES EXCEPTING ANY SIDE DELINEATED BY A KERB, BARRIER OR WALL.

2. SHARED AREAS SHALL BE MARKED AS FOLLOWS:
2.1. WALKWAYS WITHIN OR PARTLY WITHIN A SHARED AREA SHALL BE MARKED WITH UNBROKEN LONGITUDINAL LINES ON BOTH SIDES OF THE WALKWAY EXCEPTING ANY SIDE DELINEATED BY A KERB, BARRIER OR WALL.
2.2. OTHER VACANT NON-TRAFFICKED AREAS, WHICH MAY BE INTENTIONALLY OR UNINTENTIONALLY OBSTRUCTED (E.G. BY UNINTENDED PARKING), SHALL BE OUTLINED WITH UNBROKEN LINES 80 TO 100 MM WIDE ON ALL SIDES EXCEPTING ANY SIDE DELINEATED BY A KERB, BARRIER OR WALL, AND MARKED WITH DIAGONAL STRIPES 150 TO 200 MM WIDE WITH SPACES 200 MM TO 300 MM BETWEEN STRIPES. THE STRIPES SHALL BE AT AN ANGLE OF 45 ±10 DEGREES TO THE SIDE OF THE SPACE.
2.3. NO SHARED AREA MARKINGS SHALL BE PLACED IN TRAFFICKED AREAS.

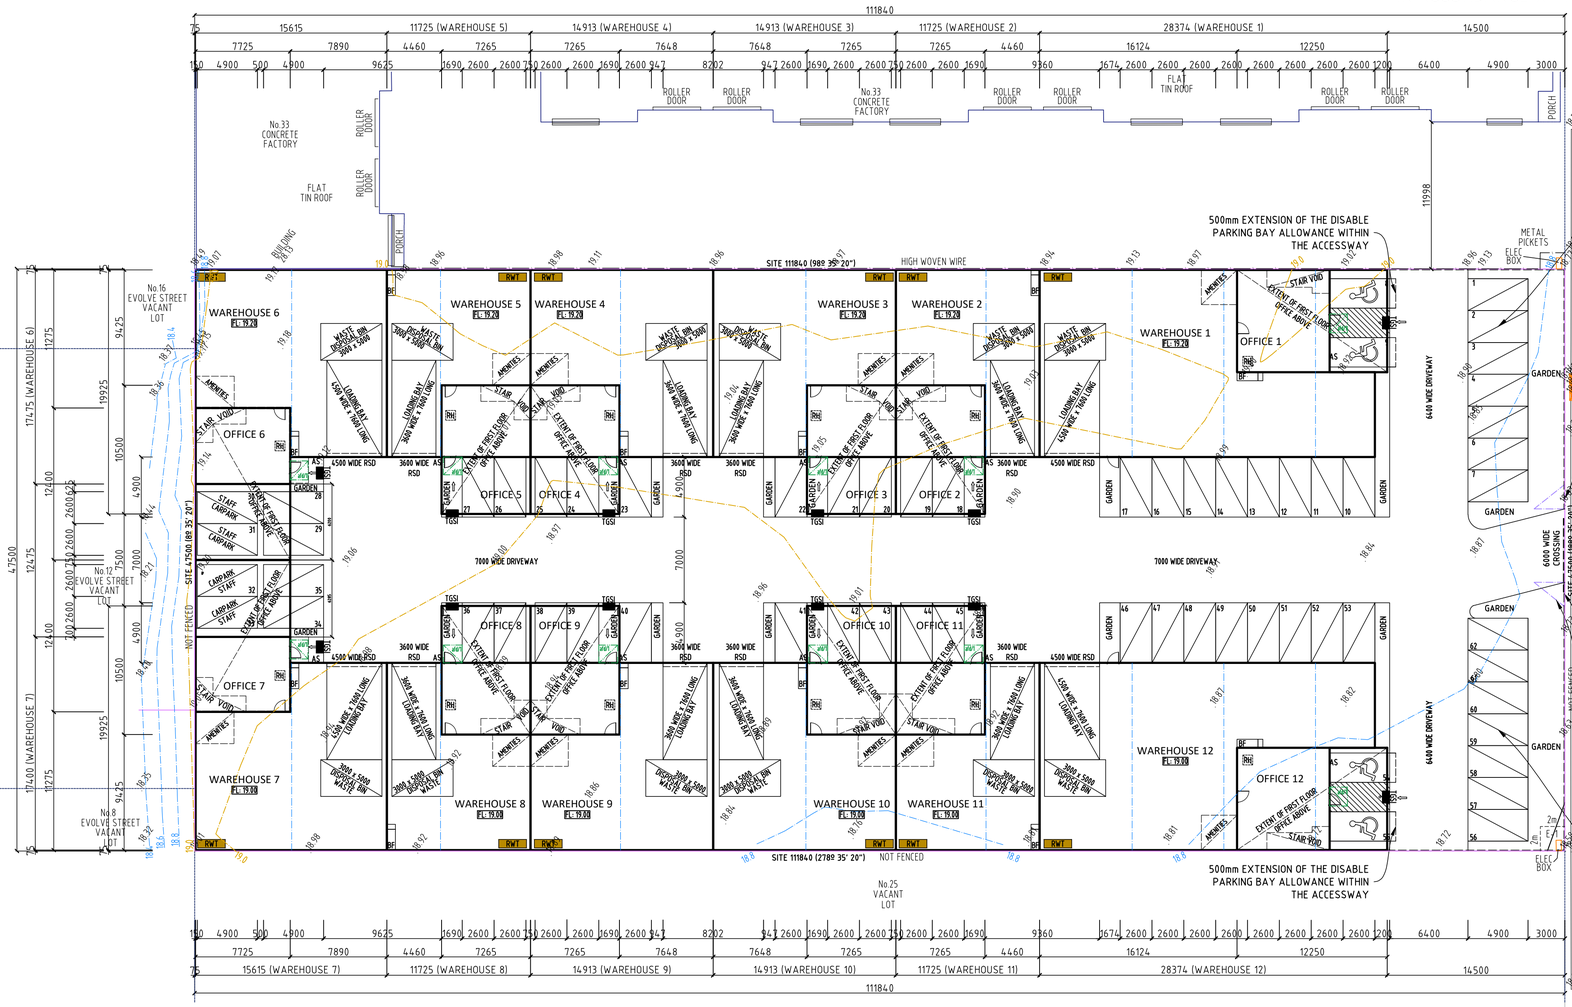




FENCE DETAIL

LEGEND

- LIGHT POLE
- TELSTRA PIT
- DRAINAGE PIT
- ELEC. PIT
- LEVELS SHOWN ON THIS PLAN ARE TO A.H.D BASED ON PAKENHAM PM 72 (R.L. 38.318)
- E-1 DENOTES A 2m WIDE POWERLINE EASEMENT
- DENOTES APPROX. VICMAP TITLE LINE
- DENOTES FIRST FLOOR BUILDING LINE
- DENOTES FIRST FLOOR HABITABLE WINDOWS
- DENOTES GROUND FLOOR HABITABLE WINDOWS

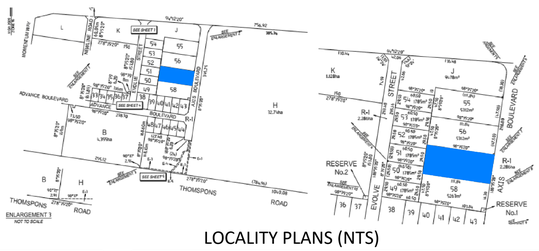

LOCALITY PLANS (NTS)

SITE DEVELOPMENT PLAN

MARKETING AREAS

REVISIONS	

THIS DRAWING AND DESIGN IS SUBJECT TO COPYRIGHT AND MAY NOT BE REPRODUCED WITHOUT PRIOR WRITTEN CONSENT FROM CREATIVE LIVING INNOVATIONS PTY LTD. CONTRACTOR TO VERIFY ALL DIMENSIONS ON SITE PRIOR TO COMMENCEMENT OF ANY WORK.
ANY DISCREPANCIES ON DRAWINGS TO BE ADVISED TO OFFICE IMMEDIATELY. FIGURED DIMENSIONS TO TAKE PRECEDENCE TO SCALED DRAWINGS.
NOTE: PLANS ARE NOT TO BE SCALED.

PRINTS A1 @ 1:250 A3 @ 1:500

PROJECT

PROPOSED WAREHOUSE AND OFFICE DEVELOPMENT
AT LOT 57, 29 AXIS BOULEVARD
OFFICER SOUTH

CLIENT

NHPB HOLDINGS PTY LTD

NORTH POINT

CREATIVE LIVING INNOVATIONS PTY LTD
SUITE 204 12-18 CORPORATE DRIVE
HEATHERTON VIC 3202
MOBILE: +61 0414 394 798
EMAIL:info@creativelivinginnovations.com.au

DATE: JULY '24
SCALE: 1:250 @ A1
SHEET: 1 OF 15
REVISION ISSUE: -
JOB No: TP 1675/25

LANDSCAPING SCHEDULE:				
PLANT NAME	COMMON NAME	POT SIZE (mm)	H x W (m)	Q'TY
TREES:-				
A EUCALYPTUS OVATA	SWAMP GUM	45 LITRE	12.0 x 7.0	6
SHRUBS:-				
B CORREA GALBRA	ROCK CORREA	300mm TUBE	1-3 x 1-3	4
C BANKSIA MARGINATA	SILVER BANKSIA	300mm TUBE	4.0 x 4.0	44
D WESTRINGIA FRUTICOSA	NATIVE ROSEMARY	200mm TUBE	1.0 x 1.0	55
E OLEARIA LIRATA	SNOWY DAISY BUSH	200mm TUBE	1.0 x 1.0	112
F LOMANDRA LONGIFOLIA	WATTLE MAT-RUSH	200mm TUBE	1-1.5 x 1-1.5	40
GROUND COVERS:-				
G BRACHYSEMA PRAEMORSUM	BRONZE BUTTERFLY	150mm TUBE		22
H CROWEA PINK STAR		150mm TUBE		28

PLANT SPECIES 'A' TO BE MINIMUM 2.0 METRES HIGH WHEN PLANTED

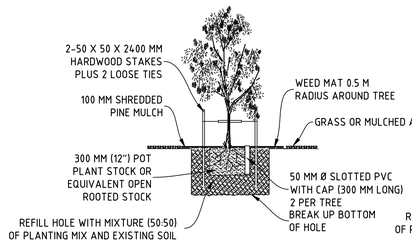


FIGURE 1


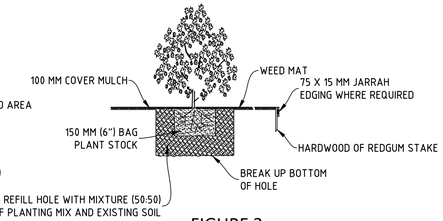


FIGURE 2

LEGEND:

- NEW CONCRETE PATHWAY OR DRIVEWAY (NATURAL GREY)
- LAWN AREA - KENTUCKY BLUE GRASS
- PROPOSED CANOPY TREE
- PROPOSED SHRUBS AND GROUND COVER PLANTING
- SIGHT TRIANGLES 2.0M X 2.5M (2500 / 2000)
- RWT 2500 LITRE RAINWATER TANK

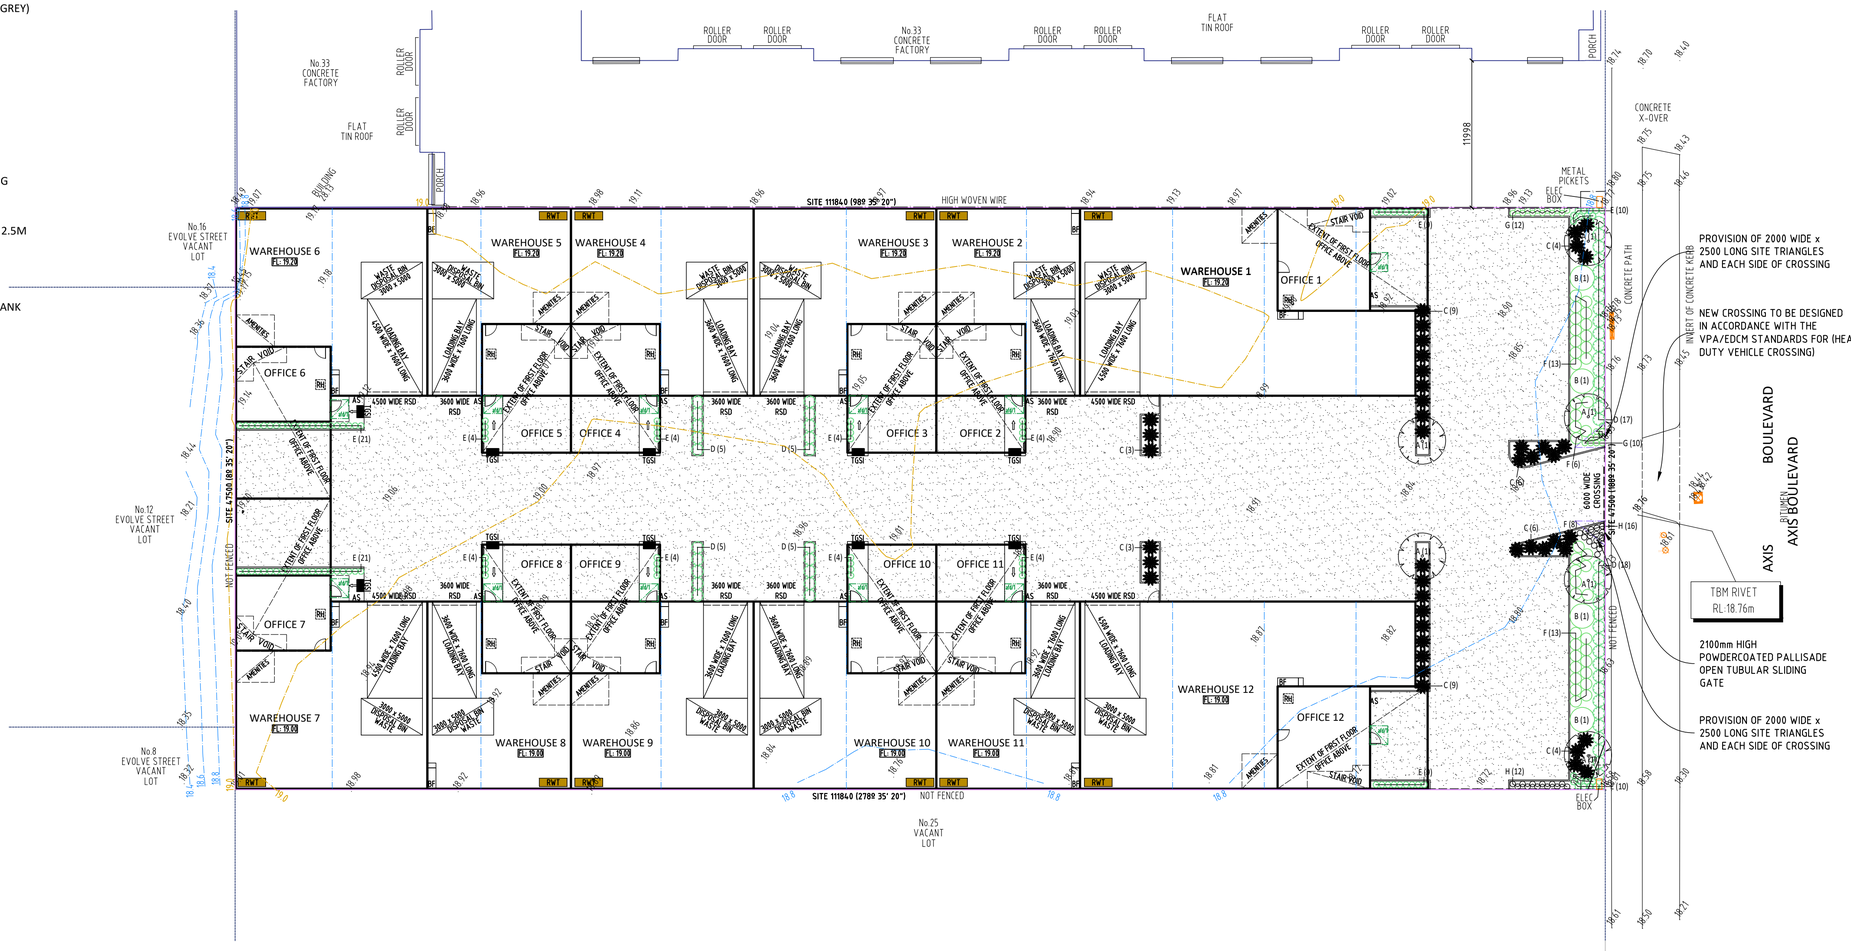

LANDSCAPE PLAN

LEGEND

- LIGHT POLE
- TELSTRA PIT
- DRAINAGE PIT
- ELEC. PIT
- LEVELS SHOWN ON THIS PLAN ARE TO A.H.D BASED ON PAKENHAM PM 72 (R.L. 38.318)
- E-1 DENOTES A 2m WIDE POWERLINE EASEMENT
- DENOTES APPROX. VICMAP TITLE LINE
- DENOTES FIRST FLOOR BUILDING LINE
- DENOTES FIRST FLOOR HABITABLE WINDOWS
- DENOTES GROUND FLOOR HABITABLE WINDOWS

LANDSCAPING NOTES:

SITE PREPARATION:-
WHERE THE SITE IS GRASSED OR HEAVILY WEEDED, THE AREA WHERE LANDSAPING IS TO OCCUR SHALL BE SPRAYED WITH ROUND UP OR SIMILAR APPROVED PRODUCT. THE EXTENT AND AMOUNT TO USE IS TO BE DETERMINED IN ACCORDANCE WITH THE SITE CONDITIONS AND RECOMMENDATION OF THE MANUFACTURER SPECIFICATIONS.

MAINTENANCE AND ESTABLISHED PERIOD:-
MAINTENANCE TO BE PROVIDED DURING THE ESTABLISHED PERIOD, ONCE PER FORTNIGHT AND THEREAFTER ON A MONTHLY BASIS FOR A PERIOD OF 3 MONTHS. HAND WATERING OF NEWLY PLANTED SHRUBS TO BE DONE ONCE PER WEEK DURING THE ESTABLISHMENT PERIOD. THIS MAY VARY ACCORDING TO THE TIME OF THE YEAR WHEN PLANTING OCCURS.
MAINTENANCE TO ALL PLANTING, GRASS AREAS TO BE REGULARLY CHECKED FOR PESTS AND DESEASES, WITH APPROPIATE TREATMENTS ARE TO BE APPLIED WHERE NECESSARY.
DURING THE COURSE OF THE YEAR, ADDITIONAL APPLICATIONS OF OSMOCOTE TO BE APPLIED IN ACCORDANCE WITH MANUFACTURER REQUIREMENTS.
ALL LAWN AREAS TO BE REGULARLY MOWED AT LEAST ONCE A MONTH DURING THE WINTER SEASON AND FORTNIGHTLY DURING THE SUMMER SEASON.

LAWN AREAS:-
WHERE INDICATED ON THE LANDSCAPE PLAN, ALL SUBGRADES TO BE CULTIVATED TO A DEPTH OF 100MM FOLLOWING APPLICATION OF GYPSUM TO CLAY SOILS AT A RATE OF 2KG/M2. SOIL TO BE SPREAD TO A EVEN THICKNESS OF 50MM, AND SUCH SOIL TO BE FREE OF PERENIAL WEEDS AND THEIR ROOTS, BULBS, AND BE A LIGHT TEXTURE, SANDY LOAM AND FREE FROM SILT OR CLAY MATERIALS.
AT PERIMETER OF LAWN AREAS PROVIDE MINIMUM 75MM HIGH JARRAH EDGING AND USE STENOTAPHRUM SECUNDATUM - SIR WALTER TURF GRASS, PLACED AND MAINTAINED IN ACCORDANCE WITH MANUFACTURER REQUIREMENTS.

SHRUB PLANTING AREAS:-
ALL SUBGRADES TO BE ROTARY HOED TO A DEPTH OF 100MM. IF CLAY IS PRESENT ADD GYPSUM TO THE SOIL TO THE MANUFACTURER RECOMMENDATIONS. WHEN ALL PLANTING IS PLACED PROVIDE TO ALL GARDEN BEDS 100MM LAYER OF FINE SHREADED PINE MULCH.
ALL PLANT SPECIES TO BE HAS NOTED WITHIN THE LANDSCAPE PLAN AND SCHEDULE, INCLUDING MATURE HEIGHTS REQUIREMENTS ON PLANTS AND QUANTITIES.
ALL PLANTING TO BE HEALTHY AND NURSURY TYPE AND FREE FROM ANY DEFECTS AND DESEASES.

IRRIGATION:-
PROVIDE DRIP IRRIGATION TO ALL TREE AND SHRUB AREAS. SUCH SYSTEM TO NE PROVIDED WITH A BATTERY OPERATED TIMER AND PROVIDED WITH 25MM PIPING FOR LONG RUNS, AND 19MM PIPING FOR SHORT RUNS.
SUCH PIPE WORK TO BE CONNECTED TO A MINIMUM 5000 LITRE RAINWATER TANK AND PROVIDED WITH A SUITABLE PUMP THAT WILL ENABLE WATER FLOW TO ALL LANDSCAPED AREAS.

MULCHED AREAS:
PROVIDE TO ALL GARDEN BEDS M20 RECYCLED PALLET MULCH. PROVIDE A MINIMUM OF 100MM LAYER OF MULCH TO ALL GARDEN BEDS.

WATER SENSITIVE URBAN DESIGN MEASURES:
PROVIDE A MINIMUM OF A 2500 LITRE ABOVE GROUND RAINWATER TANKS TO CAPTURE 100M2 OF ROOF AREA, WITH SUCH WATER USED FOR IRRIGATION USE AND FOR TOILET FLUSHING WITHIN THE PREMISES. PROVIDE A OVERFLOW PIPE TO THE LAST RAINWATER TANK AND CONNECT TO THE UNDERGROUND STORMWATER SYSTEM, HAS NOTED ON THE ATTACHED DETAIL.

REVISIONS

THIS DRAWING AND DESIGN IS SUBJECT TO COPYRIGHT AND MAY NOT BE REPRODUCED WITHOUT PRIOR WRITTEN CONSENT FROM CREATIVE LIVING INNOVATIONS PTY LTD. CONTRACTOR TO VERIFY ALL DIMENSIONS ON SITE PRIOR TO COMMENCEMENT OF ANY WORK.
ANY DISCREPANCIES ON DRAWINGS TO BE ADVISED TO OFFICE IMMEDIATELY. FIGURED DIMENSIONS TO TAKE PRECEDENCE TO SCALED DRAWINGS.
NOTE: PLANS ARE NOT TO BE SCALED.

PRINTS A1 @ 1:250 A3 @ 1:500

PROJECT

PROPOSED WAREHOUSE AND OFFICE DEVELOPMENT
AT LOT 57, 29 AXIS BOULEVARD
OFFICER SOUTH

CLIENT

NHPB HOLDINGS PTY LTD

NORTH POINT

CREATIVE LIVING INNOVATIONS PTY LTD
SUITE 204 12-18 CORPORATE DRIVE
HEATHERTON VIC 3202
MOBILE: +61 0414 394 798
EMAIL:info@creativelivinginnovations.com.au

DATE: JULY '24
SCALE: 1:250 @ A1
SHEET: 2 OF 15
REVISION ISSUE: -
JOB No: TP 1675/25


LEGEND:

DENOTES ACCESS PATH FOR ACCESS FOR DISABLED AT ENTRY TO BUILDING

DENOTES ACCESS PATH FOR ACCESS FOR DISABLED AT ENTRY TO DISABLED WC

DENOTES ACCESS PATH FOR ACCESS FOR DISABLED AT ENTRY TO AMBULANT WC

ACCESS FOR DISABLED CIRCULATION SPACE:

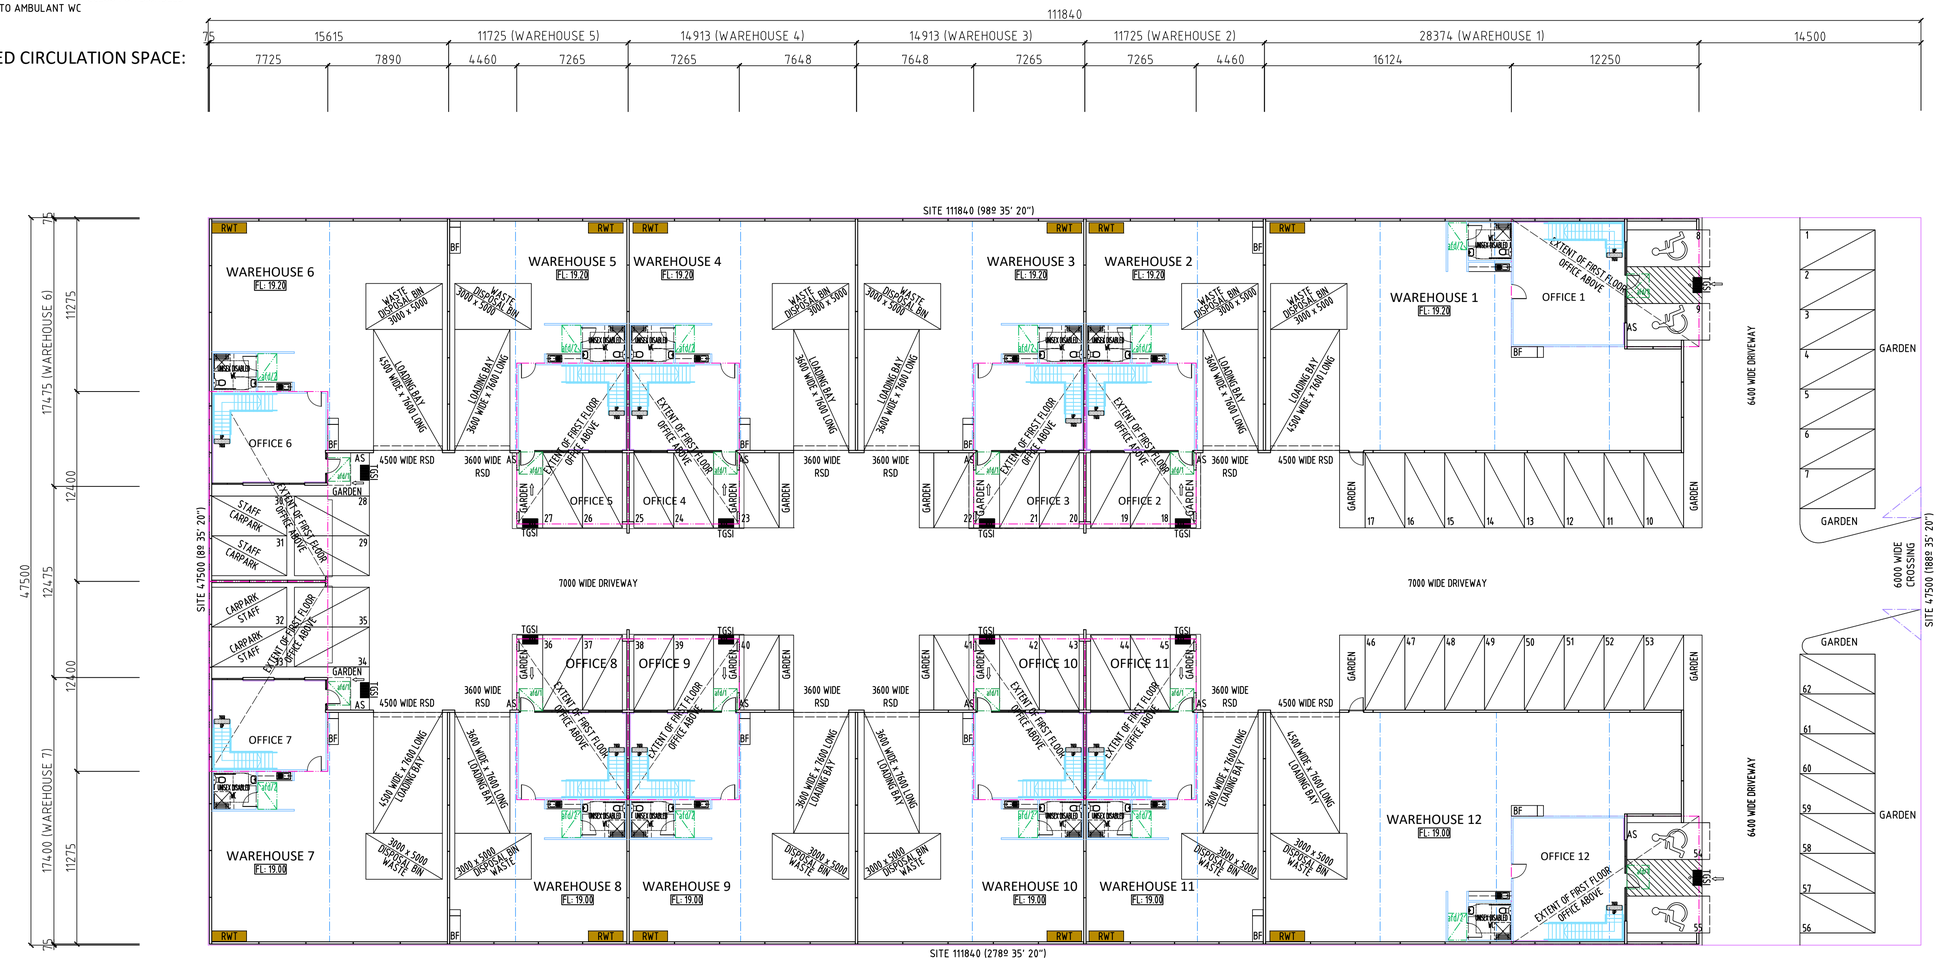

GROUND FLOOR AND SITE DEVELOPMENT PLAN

REVISIONS	

THIS DRAWING AND DESIGN IS SUBJECT TO COPYRIGHT AND MAY NOT BE REPRODUCED WITHOUT PRIOR WRITTEN CONSENT FROM CREATIVE LIVING INNOVATIONS PTY LTD. CONTRACTOR TO VERIFY ALL DIMENSIONS ON SITE PRIOR TO COMMENCEMENT OF ANY WORK. ANY DISCREPANCIES ON DRAWINGS TO BE ADVISED TO OFFICE IMMEDIATELY. FIGURED DIMENSIONS TO TAKE PRECEDENCE TO SCALED DRAWINGS. NOTE: PLANS ARE NOT TO BE SCALED.

PRINTS A1 @ 1:200 A3 @ 1:400

PROJECT

PROPOSED WAREHOUSE AND OFFICE DEVELOPMENT
AT LOT 57, 29 AXIS BOULEVARD
OFFICER SOUTH

CLIENT

NHPB HOLDINGS PTY LTD

NORTH POINT

CREATIVE LIVING INNOVATIONS PTY LTD
SUITE 204 12-18 CORPORATE DRIVE
HEATHERTON VIC 3202
MOBILE: +61 0414 394 798
EMAIL:info@creativelivinginnovations.com.au

DATE: JULY '24

SCALE: 1:200 @ A1

SHEET: 3 OF 15

REVISION ISSUE: -

JOB No: TP 1675/25

LEGEND:



DENOTES ACCESS PATH FOR ACCESS FOR DISABLED AT ENTRY TO BUILDING





DENOTES ACCESS PATH FOR ACCESS FOR DISABLED AT ENTRY TO DISABLED WC



DENOTES ACCESS PATH FOR ACCESS FOR DISABLED AT ENTRY TO AMBULANT WC

ACCESS FOR DISABLED CIRCULATION SPACE:

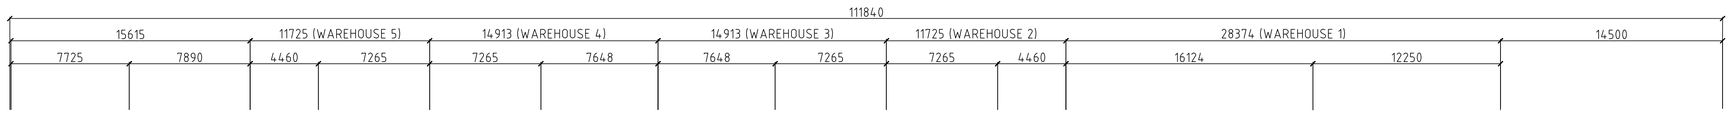

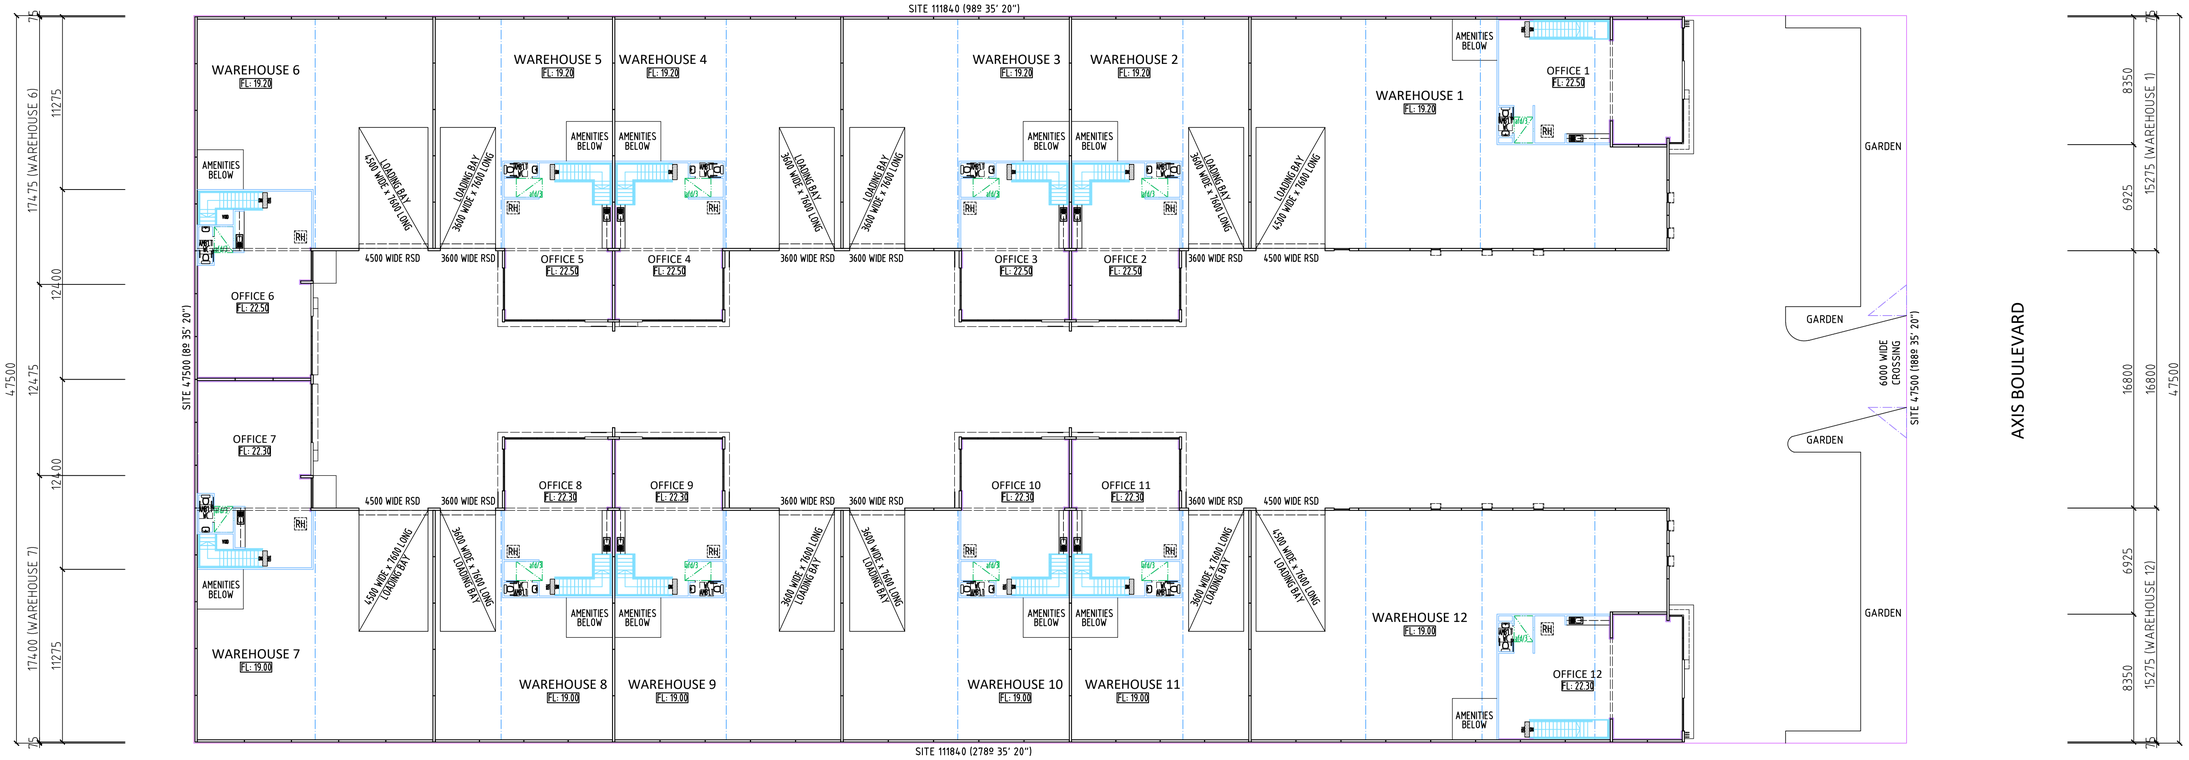

FIRST FLOOR AND SITE DEVELOPMENT PLAN

REVISIONS	

THIS DRAWING AND DESIGN IS SUBJECT TO COPYRIGHT AND MAY NOT BE REPRODUCED WITHOUT PRIOR WRITTEN CONSENT FROM CREATIVE LIVING INNOVATIONS PTY LTD. CONTRACTOR TO VERIFY ALL DIMENSIONS ON SITE PRIOR TO COMMENCEMENT OF ANY WORK.
ANY DISCREPANCIES ON DRAWINGS TO BE ADVISED TO OFFICE IMMEDIATELY. FIGURED DIMENSIONS TO TAKE PRECEDENCE TO SCALED DRAWINGS.
NOTE: PLANS ARE NOT TO BE SCALED.

PRINTS A1 @ 1:200 A3 @ 1:400

PROJECT

PROPOSED WAREHOUSE AND OFFICE DEVELOPMENT
AT LOT 57, 29 AXIS BOULEVARD
OFFICER SOUTH


CLIENT

NHPB HOLDINGS PTY LTD


NORTH POINT

CREATIVE LIVING INNOVATIONS PTY LTD
SUITE 204 12-18 CORPORATE DRIVE
HEATHERTON VIC 3202
MOBILE: +61 0414 394 798
EMAIL:info@creativelivinginnovations.com.au


DATE: JULY '24
SCALE: 1:200 @ A1
SHEET: 4 OF 15
REVISION ISSUE: -
JOB No: TP 1675/25

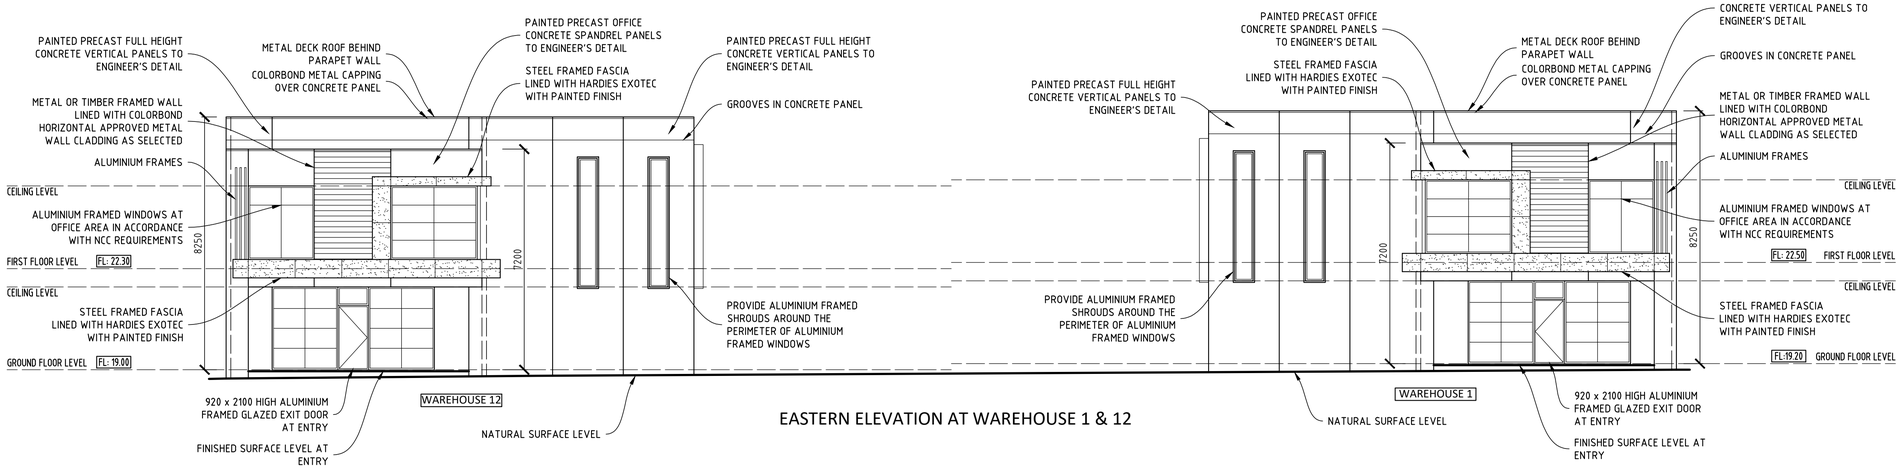


EASTERN ELEVATION AT WAREHOUSE 1 & 12

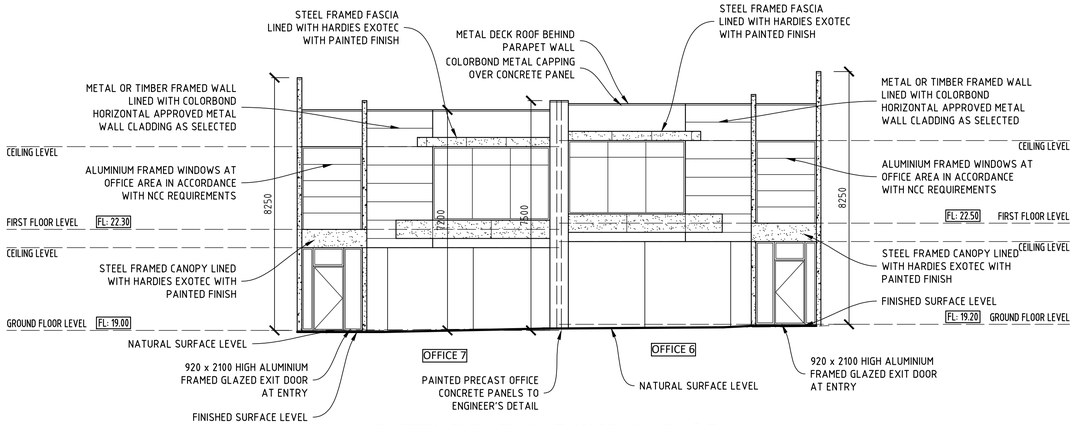

EASTERN ELEVATION AT WAREHOUSE 6 & 7

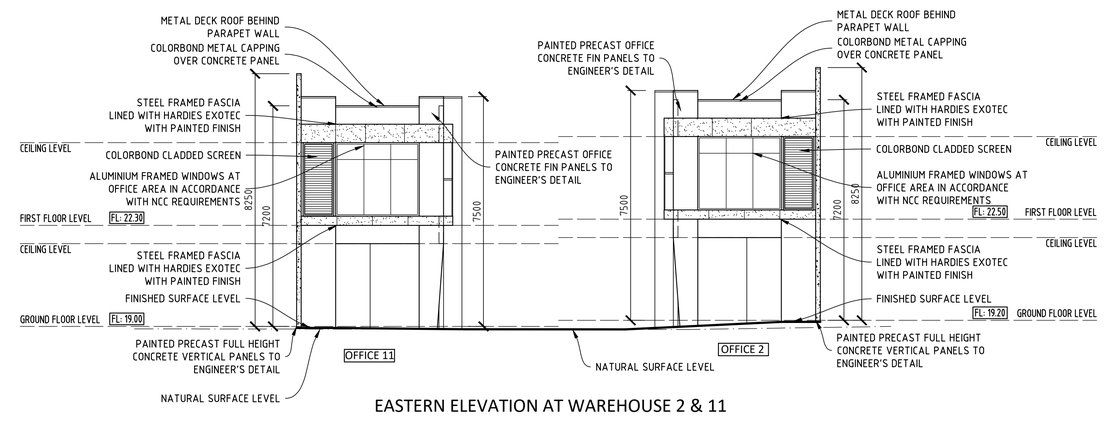

EASTERN ELEVATION AT WAREHOUSE 2 & 11

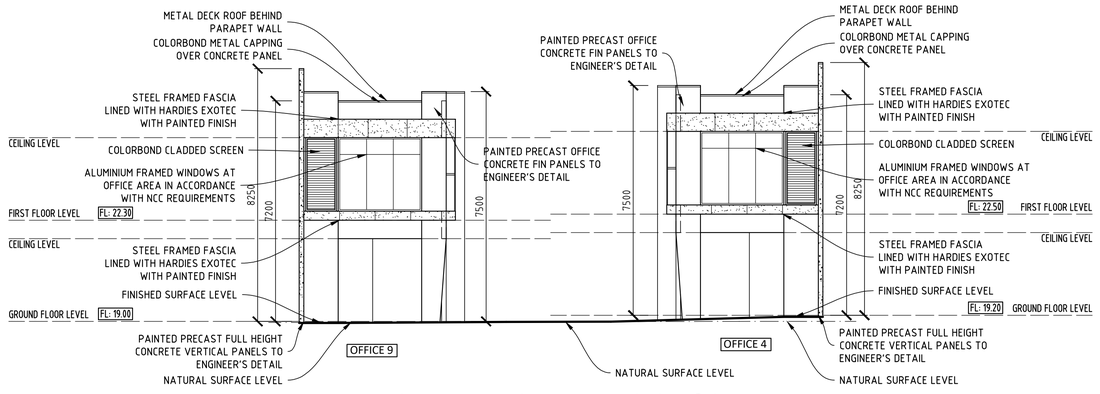

EASTERN ELEVATION AT WAREHOUSE 4 & 9

REVISIONS	

THIS DRAWING AND DESIGN IS SUBJECT TO COPYRIGHT AND MAY NOT BE REPRODUCED WITHOUT PRIOR WRITTEN CONSENT FROM CREATIVE LIVING INNOVATIONS PTY LTD. CONTRACTOR TO VERIFY ALL DIMENSIONS ON SITE PRIOR TO COMMENCEMENT OF ANY WORK.
ANY DISCREPANCIES ON DRAWINGS TO BE ADVISED TO OFFICE IMMEDIATELY. FIGURED DIMENSIONS TO TAKE PRECEDENCE TO SCALED DRAWINGS.
NOTE: PLANS ARE NOT TO BE SCALED.

PRINTS A1 @ 1:100	A3 @ 1:200

PROJECT

PROPOSED WAREHOUSE AND OFFICE DEVELOPMENT
AT LOT 57, 29 AXIS BOULEVARD
OFFICER SOUTH

CLIENT

NHPB HOLDINGS PTY LTD

NORTH POINT

CREATIVE LIVING INNOVATIONS PTY LTD
SUITE 204 12-18 CORPORATE DRIVE
HEATHERTON VIC 3202
MOBILE: +61 0414 394 798
EMAIL:info@creativelivinginnovations.com.au


DATE: JULY '24

SCALE: 1:100 @ A1


SHEET: 5 OF 15

REVISION ISSUE: -

JOB No: TP 1675/25

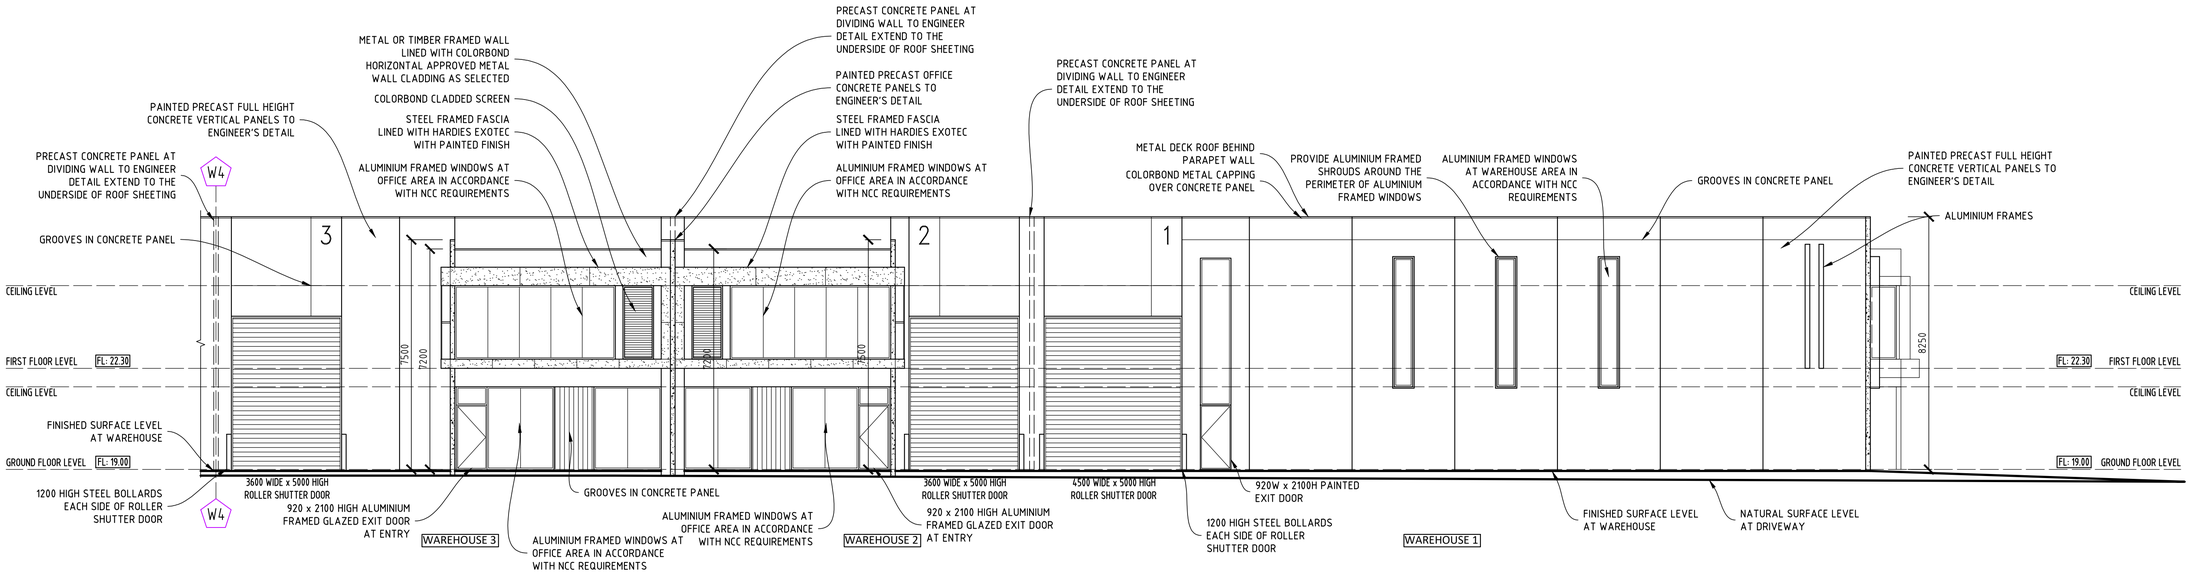

PART SOUTHERN ELEVATION AT WAREHOUSE 1-3

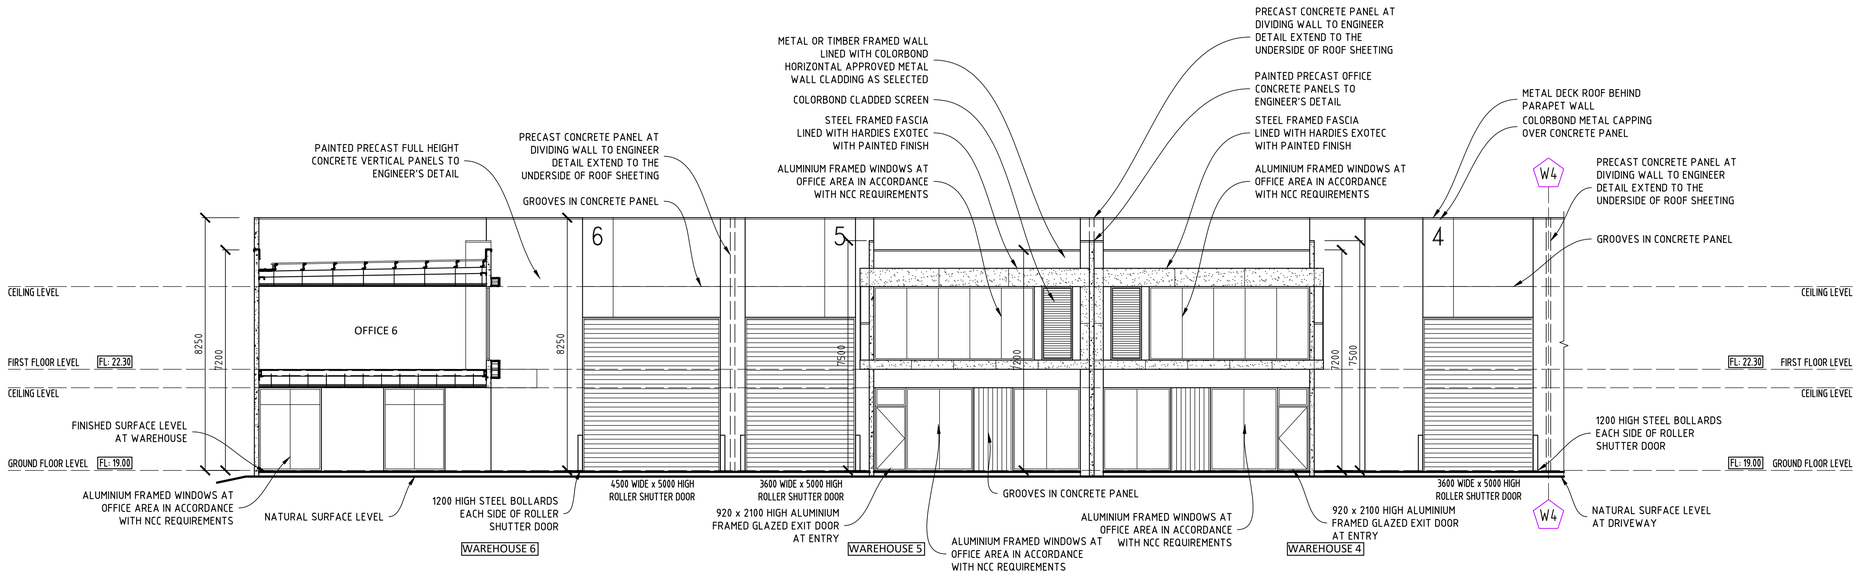

PART SOUTHERN ELEVATION AT WAREHOUSE 4-6

REVISIONS

THIS DRAWING AND DESIGN IS SUBJECT TO COPYRIGHT AND MAY NOT BE REPRODUCED WITHOUT PRIOR WRITTEN CONSENT FROM CREATIVE LIVING INNOVATIONS PTY LTD. CONTRACTOR TO VERIFY ALL DIMENSIONS ON SITE PRIOR TO COMMENCEMENT OF ANY WORK.
ANY DISCREPANCIES ON DRAWINGS TO BE ADVISED TO OFFICE IMMEDIATELY. FIGURED DIMENSIONS TO TAKE PRECEDENCE TO SCALED DRAWINGS.
NOTE: PLANS ARE NOT TO BE SCALED.

PRINTS A1 @ 1:100 A3 @ 1:200

PROJECT

PROPOSED WAREHOUSE AND OFFICE DEVELOPMENT
AT LOT 57, 29 AXIS BOULEVARD
OFFICER SOUTH

CLIENT

NHPB HOLDINGS PTY LTD

NORTH POINT

CREATIVE LIVING INNOVATIONS PTY LTD
SUITE 204 12-18 CORPORATE DRIVE
HEATHERTON VIC 3202
MOBILE: +61 0414 394 798
EMAIL:info@creativelivinginnovations.com.au


DATE: JULY '24

SCALE: 1:100 @ A1


SHEET: 6 OF 15

REVISION ISSUE: -

JOB No: TP 1675/25

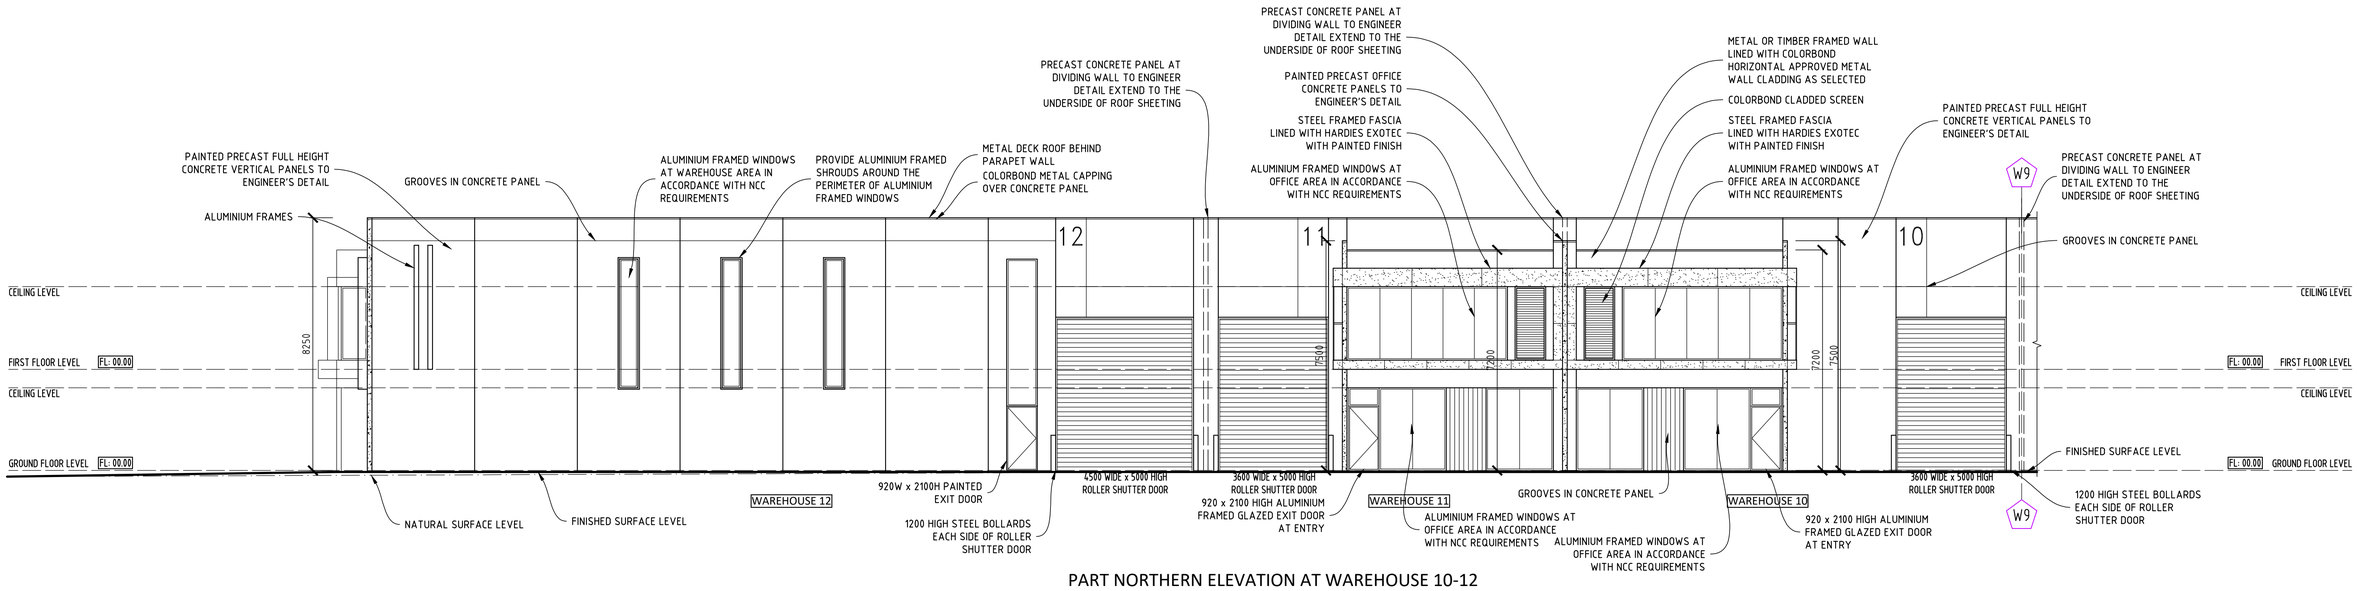

PART NORTHERN ELEVATION AT WAREHOUSE 10-12

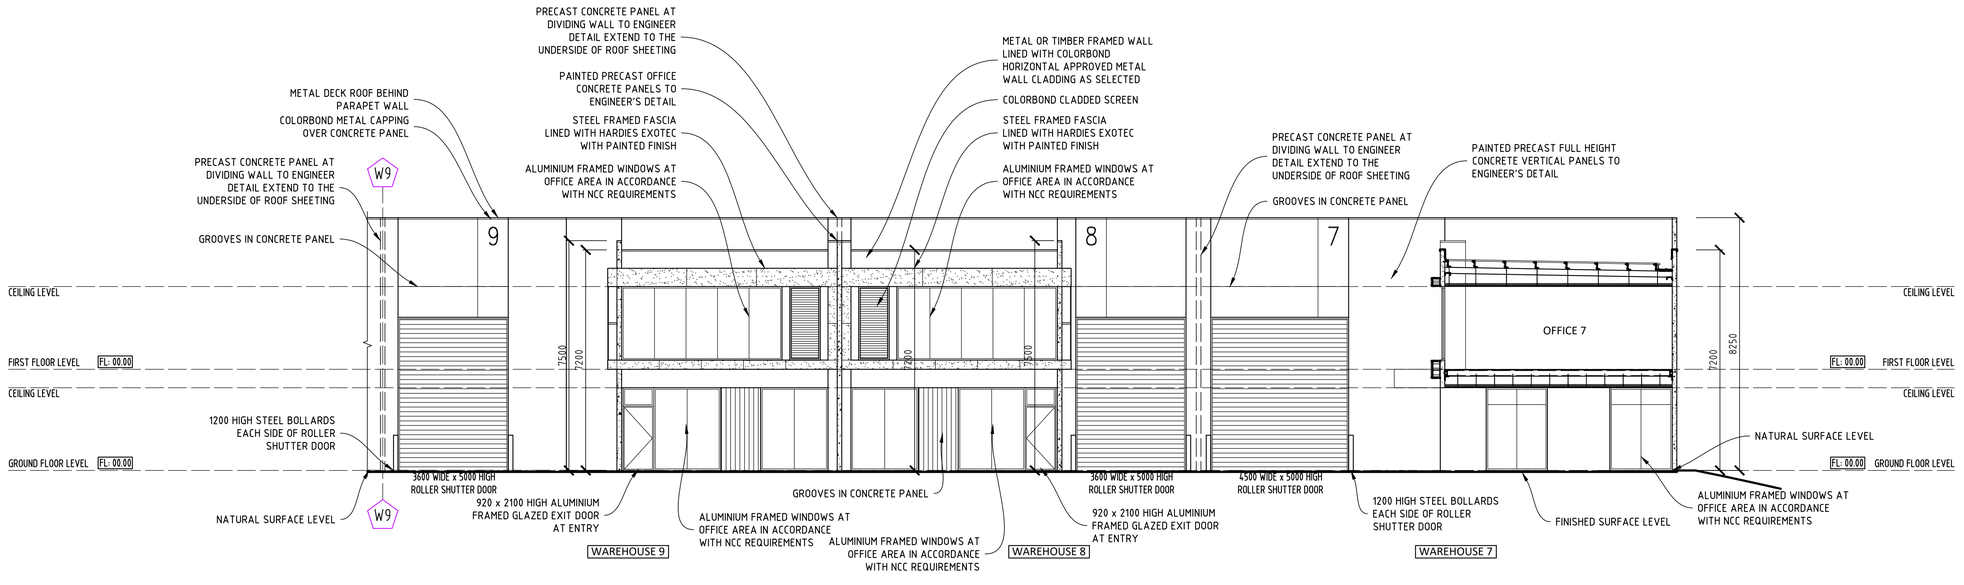

PART NORTHERN ELEVATION AT WAREHOUSE 7-9

REVISIONS

THIS DRAWING AND DESIGN IS SUBJECT TO COPYRIGHT AND MAY NOT BE REPRODUCED WITHOUT PRIOR WRITTEN CONSENT FROM CREATIVE LIVING INNOVATIONS PTY LTD. CONTRACTOR TO VERIFY ALL DIMENSIONS ON SITE PRIOR TO COMMENCEMENT OF ANY WORK.
ANY DISCREPANCIES ON DRAWINGS TO BE ADVISED TO OFFICE IMMEDIATELY. FIGURED DIMENSIONS TO TAKE PRECEDENCE TO SCALED DRAWINGS.
NOTE: PLANS ARE NOT TO BE SCALED.

PRINTS A1 @ 1:100 A3 @ 1:200

PROJECT

PROPOSED WAREHOUSE AND OFFICE DEVELOPMENT
AT LOT 57, 29 AXIS BOULEVARD
OFFICER SOUTH


CLIENT

NHPB HOLDINGS PTY LTD


NORTH POINT

CREATIVE LIVING INNOVATIONS PTY LTD
SUITE 204 12-18 CORPORATE DRIVE
HEATHERTON VIC 3202
MOBILE: +61 0414 394 798
EMAIL:info@creativelivinginnovations.com.au


DATE: JULY '24
SCALE: 1:100 @ A1
SHEET: 7 OF 15
REVISION ISSUE: -
JOB No: TP 1675/25

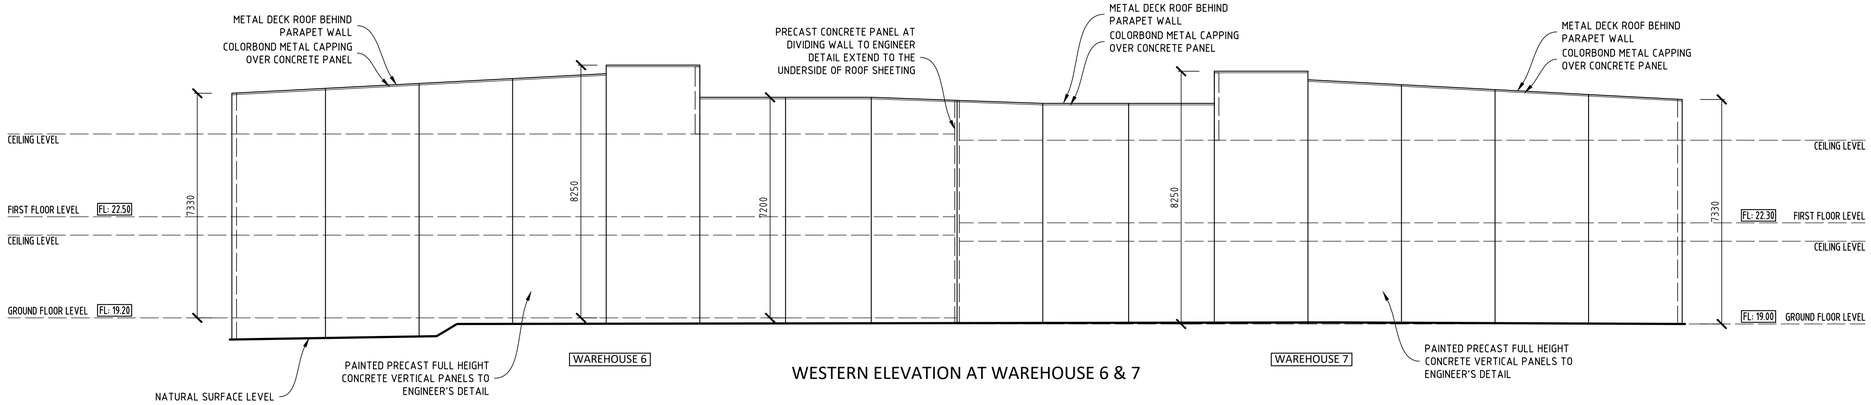

WESTERN ELEVATION AT WAREHOUSE 6 & 7

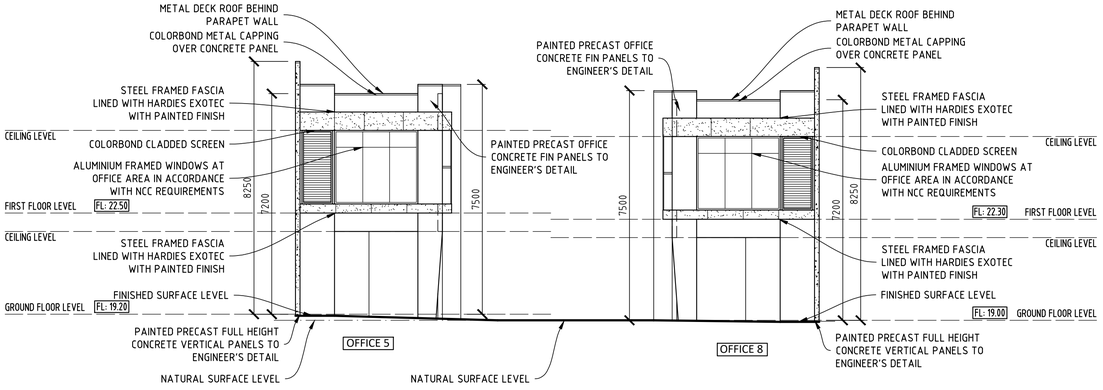

WESTERN ELEVATION AT WAREHOUSE 5 & 8

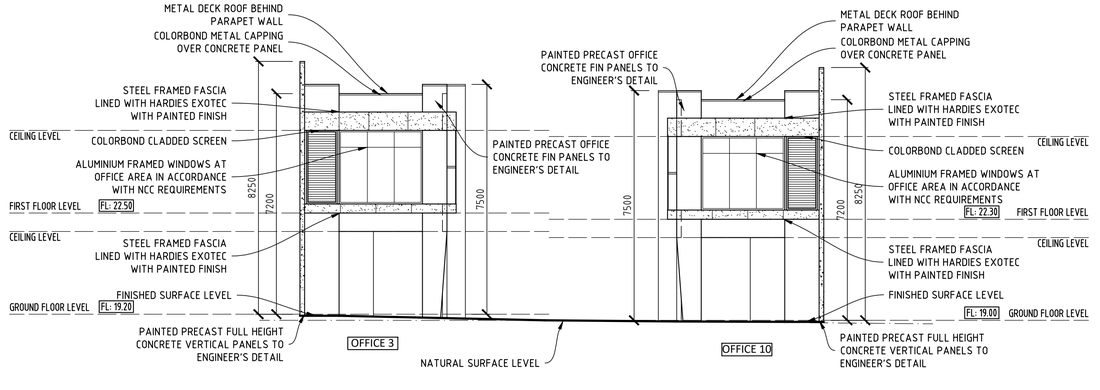

WESTERN ELEVATION AT WAREHOUSE 3 & 10

REVISIONS

THIS DRAWING AND DESIGN IS SUBJECT TO COPYRIGHT AND MAY NOT BE REPRODUCED WITHOUT PRIOR WRITTEN CONSENT FROM CREATIVE LIVING INNOVATIONS PTY LTD. CONTRACTOR TO VERIFY ALL DIMENSIONS ON SITE PRIOR TO COMMENCEMENT OF ANY WORK.
ANY DISCREPANCIES ON DRAWINGS TO BE ADVISED TO OFFICE IMMEDIATELY. FIGURED DIMENSIONS TO TAKE PRECEDENCE TO SCALED DRAWINGS.
NOTE: PLANS ARE NOT TO BE SCALED.

PRINTS A1 @ 1:100 A3 @ 1:200

PROJECT

PROPOSED WAREHOUSE AND OFFICE DEVELOPMENT
AT LOT 57, 29 AXIS BOULEVARD
OFFICER SOUTH

CLIENT

NHPB HOLDINGS PTY LTD

NORTH POINT

CREATIVE LIVING INNOVATIONS PTY LTD
SUITE 204 12-18 CORPORATE DRIVE
HEATHERTON VIC 3202
MOBILE: +61 0414 394 798
EMAIL:info@creativelivinginnovations.com.au


DATE: JULY '24

SCALE: 1:100 @ A1


SHEET: 8 OF 15

REVISION ISSUE: -

JOB No: TP 1675/25

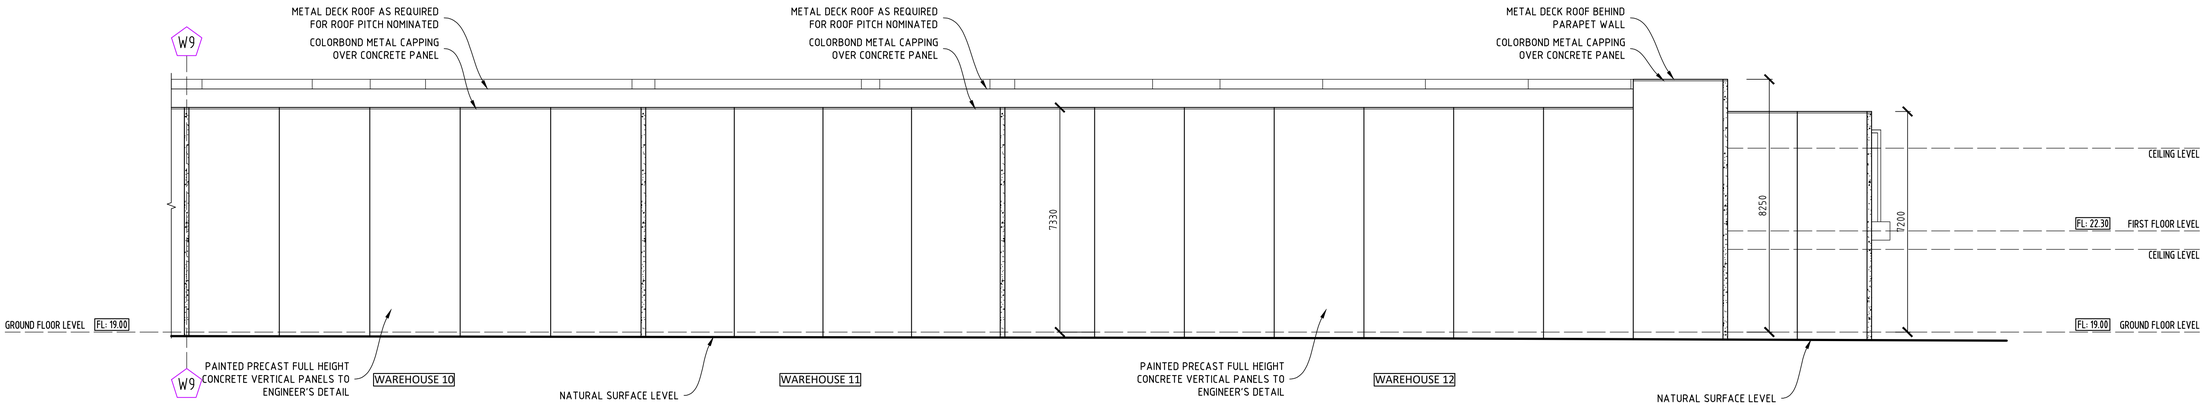

PART SOUTHERN ELEVATION AT WAREHOUSE 10-12

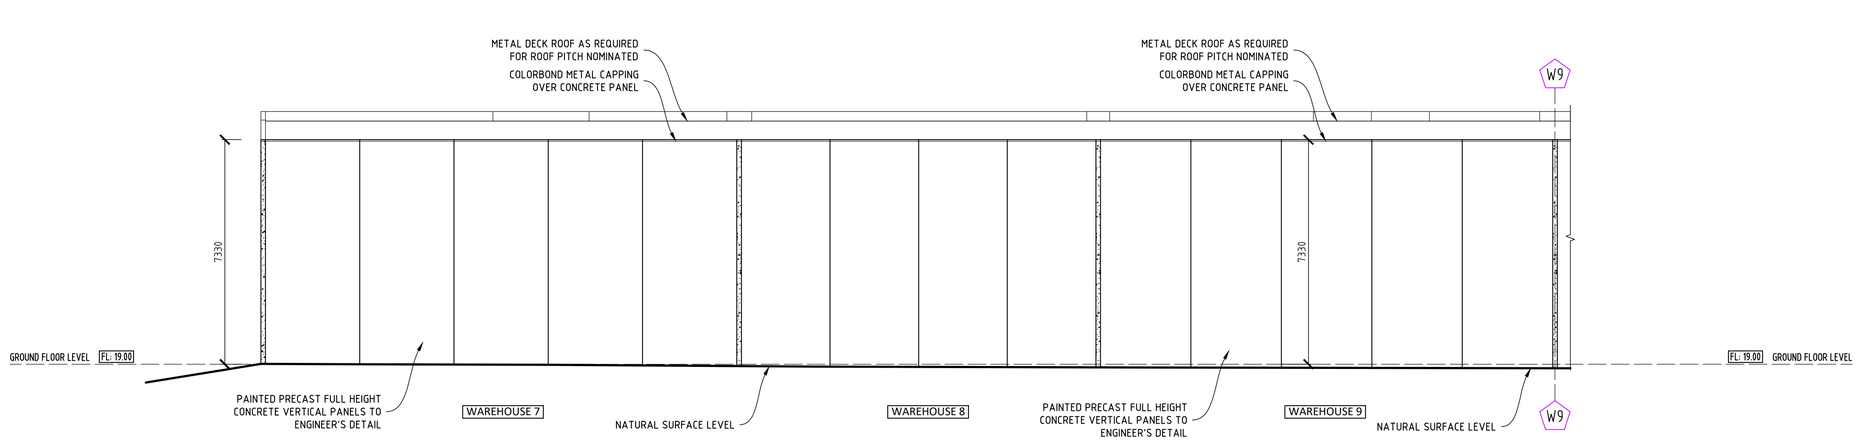

SOUTHERN ELEVATION AT WAREHOUSE 7-9

REVISIONS

THIS DRAWING AND DESIGN IS SUBJECT TO COPYRIGHT AND MAY NOT BE REPRODUCED WITHOUT PRIOR WRITTEN CONSENT FROM CREATIVE LIVING INNOVATIONS PTY LTD. CONTRACTOR TO VERIFY ALL DIMENSIONS ON SITE PRIOR TO COMMENCEMENT OF ANY WORK.
ANY DISCREPANCIES ON DRAWINGS TO BE ADVISED TO OFFICE IMMEDIATELY. FIGURED DIMENSIONS TO TAKE PRECEDENCE TO SCALED DRAWINGS.
NOTE: PLANS ARE NOT TO BE SCALED.

PRINTS A1 @ 1:100 A3 @ 1:200

PROJECT

PROPOSED WAREHOUSE AND OFFICE DEVELOPMENT
AT LOT 57, 29 AXIS BOULEVARD
OFFICER SOUTH


CLIENT

NHPB HOLDINGS PTY LTD


NORTH POINT

CREATIVE LIVING INNOVATIONS PTY LTD
SUITE 204 12-18 CORPORATE DRIVE
HEATHERTON VIC 3202
MOBILE: +61 0414 394 798
EMAIL:info@creativelivinginnovations.com.au

DATE: JULY '24
SCALE: 1:100 @ A1
SHEET: 9 OF 15
REVISION ISSUE: -
JOB No: TP 1675/25

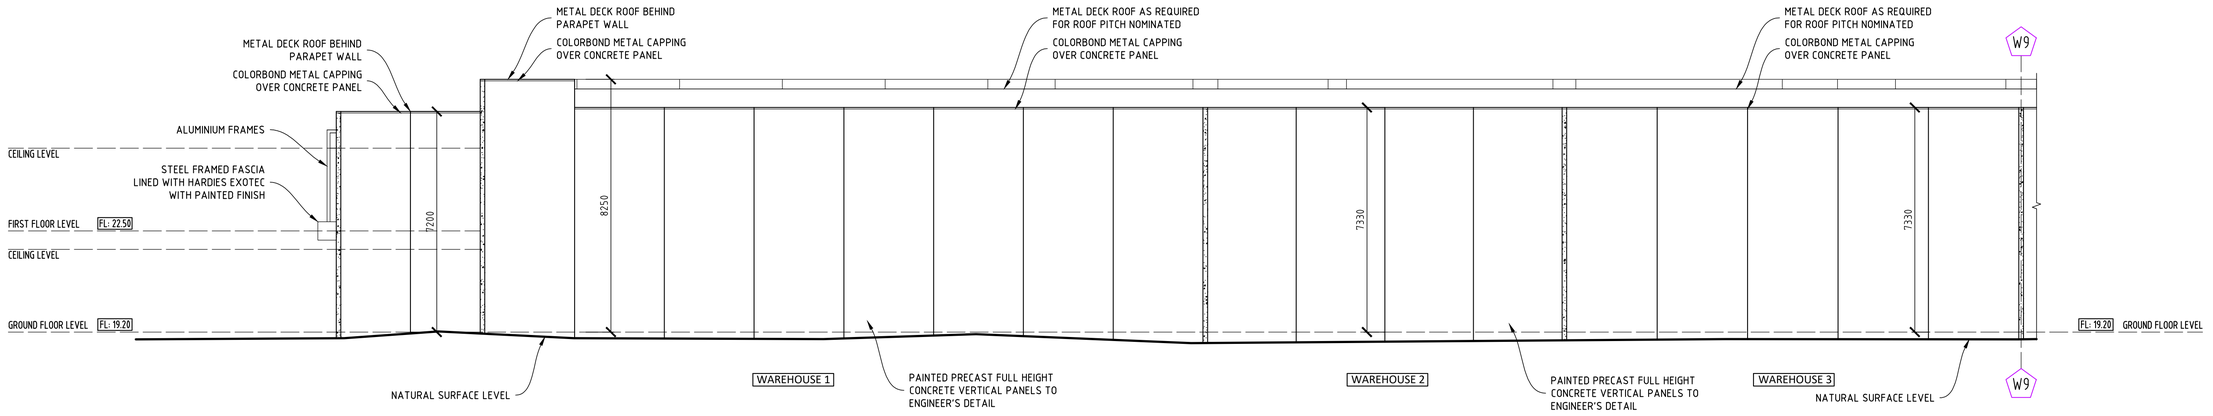

PART NORTHERN ELEVATION AT WAREHOUSE 1-3

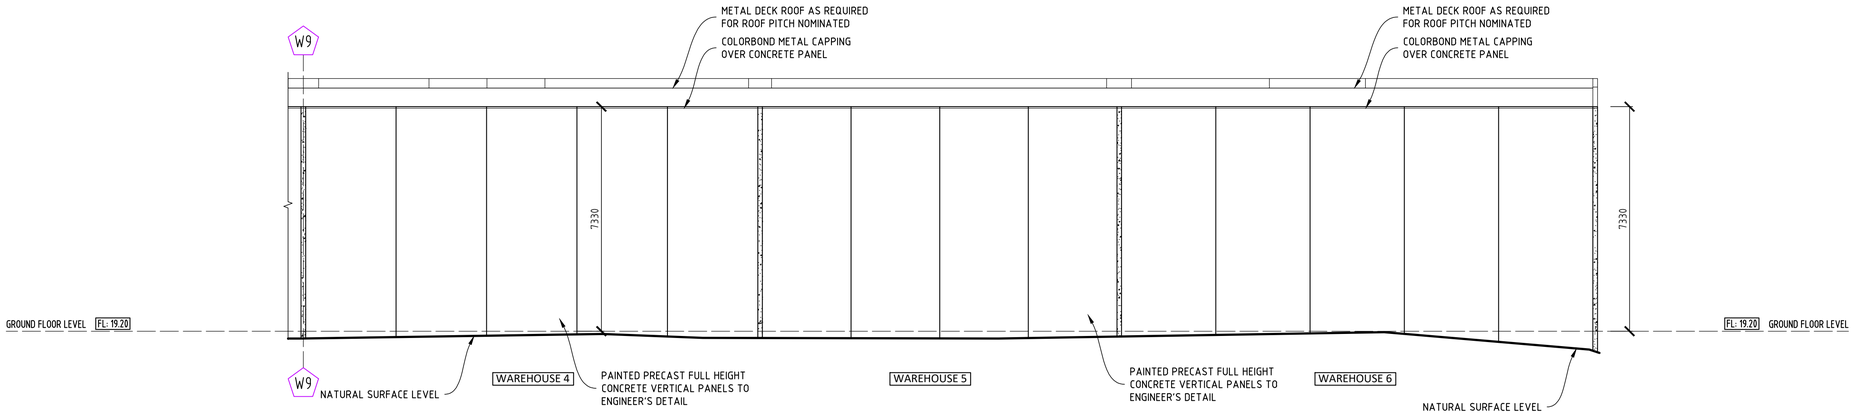

SOUTHERN ELEVATION AT WAREHOUSE 4-6

REVISIONS

THIS DRAWING AND DESIGN IS SUBJECT TO COPYRIGHT AND MAY NOT BE REPRODUCED WITHOUT PRIOR WRITTEN CONSENT FROM CREATIVE LIVING INNOVATIONS PTY LTD. CONTRACTOR TO VERIFY ALL DIMENSIONS ON SITE PRIOR TO COMMENCEMENT OF ANY WORK.
ANY DISCREPANCIES ON DRAWINGS TO BE ADVISED TO OFFICE IMMEDIATELY. FIGURED DIMENSIONS TO TAKE PRECEDENCE TO SCALED DRAWINGS.
NOTE: PLANS ARE NOT TO BE SCALED.

PRINTS A1 @ 1:100 A3 @ 1:200

PROJECT

PROPOSED WAREHOUSE AND OFFICE DEVELOPMENT
AT LOT 57, 29 AXIS BOULEVARD
OFFICER SOUTH

CLIENT

NHPB HOLDINGS PTY LTD

NORTH POINT

CREATIVE LIVING INNOVATIONS PTY LTD
SUITE 204 12-18 CORPORATE DRIVE
HEATHERTON VIC 3202
MOBILE: +61 0414 394 798
EMAIL:info@creativelivinginnovations.com.au


DATE: JULY '24

SCALE: 1:100 @ A1


SHEET: 10 OF 15

REVISION ISSUE: -


JOB No: TP 1675/25

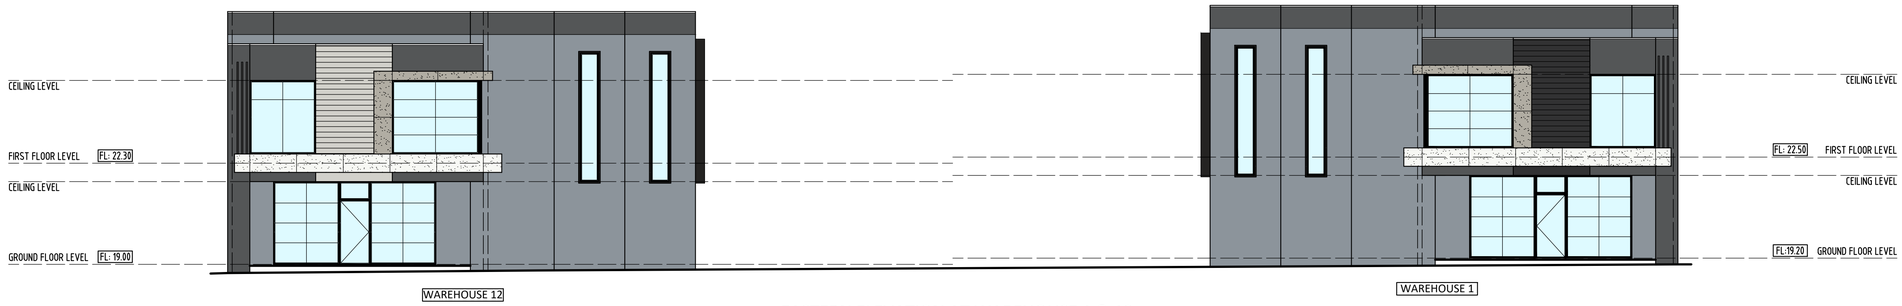


EASTERN ELEVATION AT WAREHOUSE 1 & 12

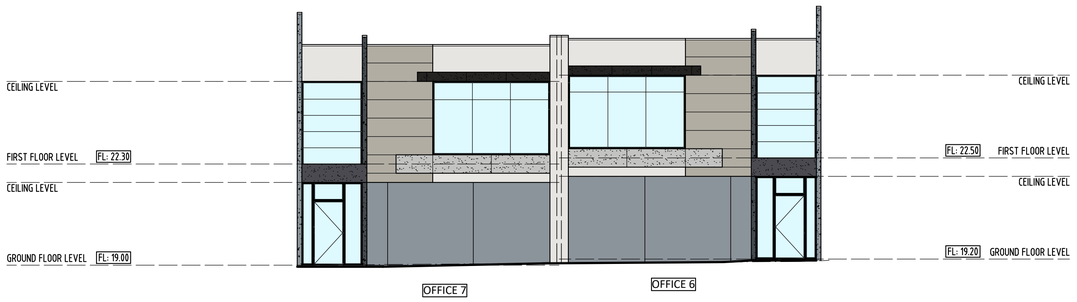

EASTERN ELEVATION AT WAREHOUSE 6 & 7

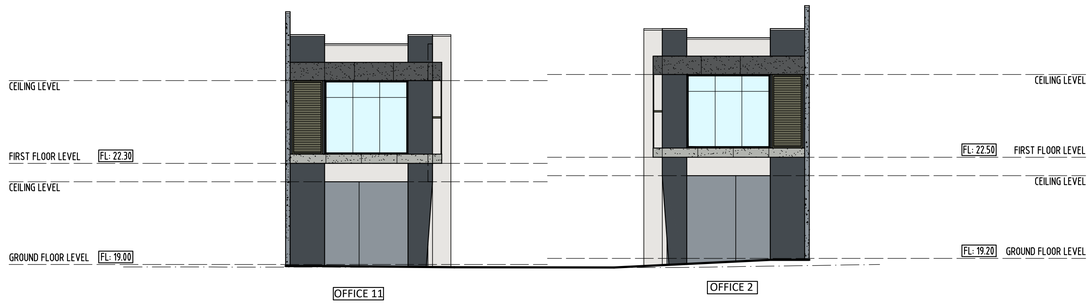

EASTERN ELEVATION AT WAREHOUSE 2 & 11

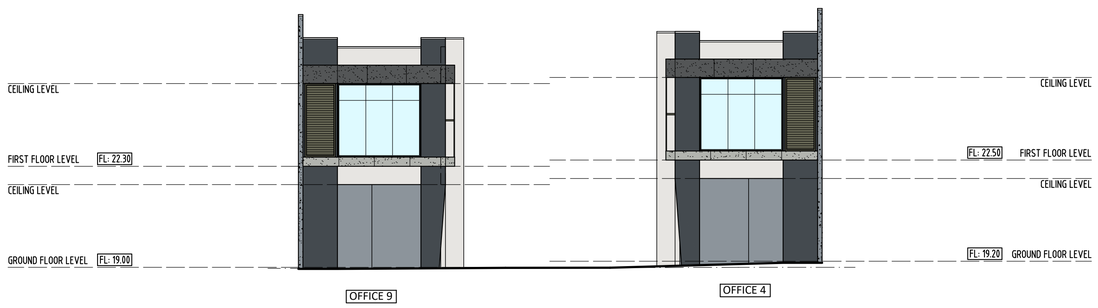

EASTERN ELEVATION AT WAREHOUSE 4 & 9

SCHEDULE OF FINISHES

WAREHOUSE CONCRETE PANELS DULUX STEEL MAGNET	OFFICE CONCRETE PANELS 3 DULUX TIMELESS GREY	LIGHTWEIGHT PANEL 1 COLORBOND MONUMENT	WINDOW/DOOR FRAMES BLACK
ROLLER DOORS COLORBOND MONUMENT	FASCIA FRAMES DULUX DUNE	LIGHTWEIGHT PANEL 2 DULUX TRANQUIL RETREAT	BOLLARDS DULUX SHARP YELLOW
WAREHOUSE PANELS 1 DULUX WESTERN MYALL	FASCIA FRAMES 1 DULUX VIVID WHITE	ALUMINIUM SHROUDS DULUX BLACK	
WAREHOUSE PANELS 2 DULUX TRANQUIL RETREAT	FASCIA FRAMES 2 DULUX BLACK	ALUMINIUM FRAMES DULUX MONUMENT	
OFFICE CONCRETE PANELS DULUX WESTERN MYALL	FASCIA FRAMES 3 DULUX SHALE GREY	CLADDED SCREEN COLORBOND MANGROVE	
OFFICE CONCRETE PANELS 1 DULUX BLISSFULL WHITE	FASCIA FRAMES 4 DULUX WESTERN MYALL	CLADDED SCREEN 2 COLORBOND DEEP OCEAN	
OFFICE CONCRETE PANELS 2 DULUX CHARCOAL FUSION	LIGHTWEIGHT PANEL COLORBOND SOUTHERLY		

REVISIONS

THIS DRAWING AND DESIGN IS SUBJECT TO COPYRIGHT AND MAY NOT BE REPRODUCED WITHOUT PRIOR WRITTEN CONSENT FROM CREATIVE LIVING INNOVATIONS PTY LTD. CONTRACTOR TO VERIFY ALL DIMENSIONS ON SITE PRIOR TO COMMENCEMENT OF ANY WORK.
ANY DISCREPANCIES ON DRAWINGS TO BE ADVISED TO OFFICE IMMEDIATELY. FIGURED DIMENSIONS TO TAKE PRECEDENCE TO SCALED DRAWINGS.
NOTE: PLANS ARE NOT TO BE SCALED.

PRINTS A1 @ 1:100 A3 @ 1:200

PROJECT

PROPOSED WAREHOUSE AND OFFICE DEVELOPMENT
AT LOT 57, 29 AXIS BOULEVARD
OFFICER SOUTH


CLIENT

NHPB HOLDINGS PTY LTD


NORTH POINT

CREATIVE LIVING INNOVATIONS PTY LTD
SUITE 204 12-18 CORPORATE DRIVE
HEATHERTON VIC 3202
MOBILE: +61 0414 394 798
EMAIL:info@creativelivinginnovations.com.au

DATE: JULY '24
SCALE: 1:100 @ A1
SHEET: 11 OF 15
REVISION ISSUE: -
JOB No: TP 1675/25

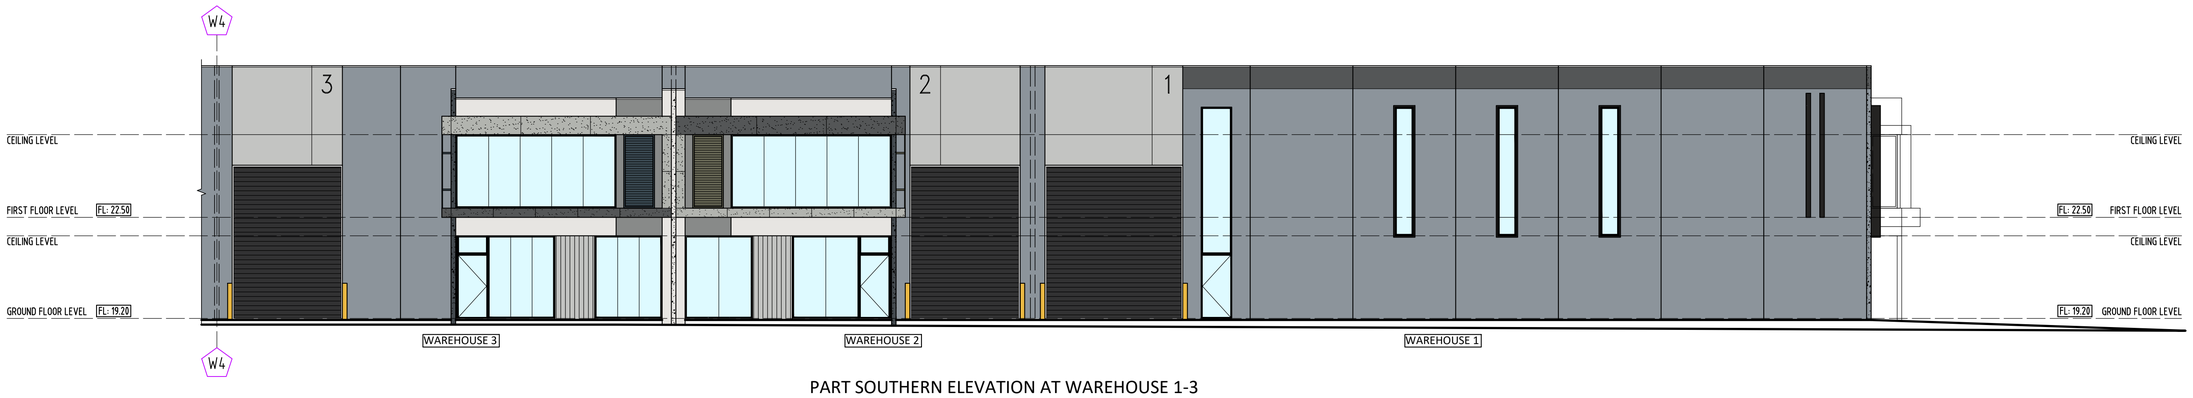

PART SOUTHERN ELEVATION AT WAREHOUSE 1-3

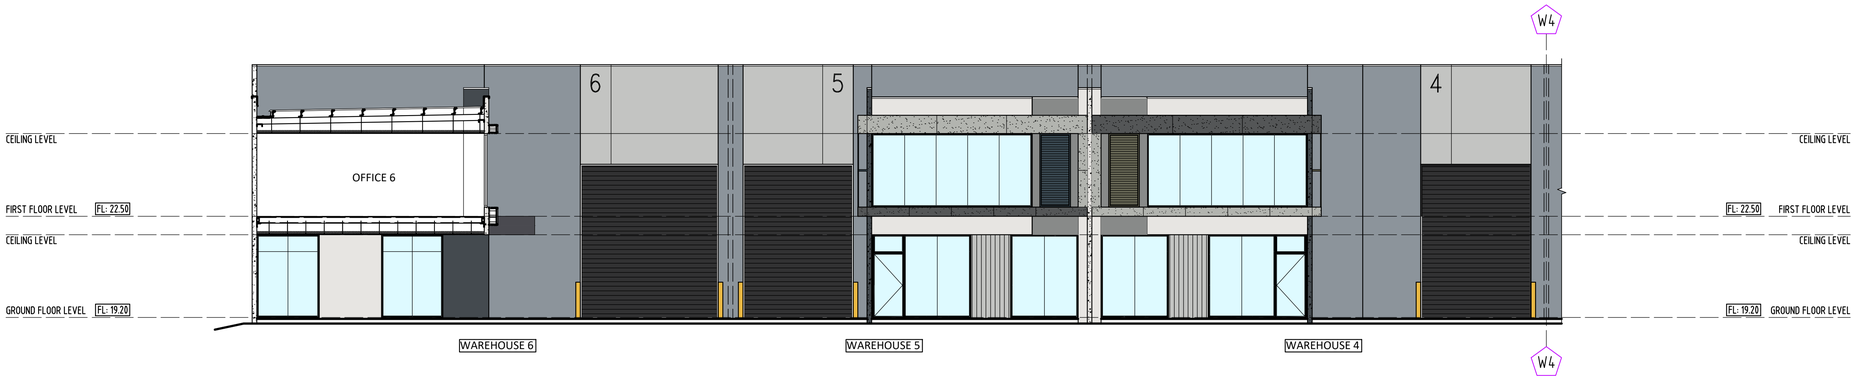

PART SOUTHERN ELEVATION AT WAREHOUSE 4-6

REVISIONS

THIS DRAWING AND DESIGN IS SUBJECT TO COPYRIGHT AND MAY NOT BE REPRODUCED WITHOUT PRIOR WRITTEN CONSENT FROM CREATIVE LIVING INNOVATIONS PTY LTD. CONTRACTOR TO VERIFY ALL DIMENSIONS ON SITE PRIOR TO COMMENCEMENT OF ANY WORK.
ANY DISCREPANCIES ON DRAWINGS TO BE ADVISED TO OFFICE IMMEDIATELY. FIGURED DIMENSIONS TO TAKE PRECEDENCE TO SCALED DRAWINGS.
NOTE: PLANS ARE NOT TO BE SCALED.

PRINTS A1 @ 1:100 A3 @ 1:200

PROJECT

PROPOSED WAREHOUSE AND OFFICE DEVELOPMENT
AT LOT 57, 29 AXIS BOULEVARD
OFFICER SOUTH


CLIENT

NHPB HOLDINGS PTY LTD


NORTH POINT

CREATIVE LIVING INNOVATIONS PTY LTD
SUITE 204 12-18 CORPORATE DRIVE
HEATHERTON VIC 3202
MOBILE: +61 0414 394 798
EMAIL:info@creativelivinginnovations.com.au


DATE: JULY '24
SCALE: 1:100 @ A1
SHEET: 12 OF 15
REVISION ISSUE: -
JOB No: TP 1675/25

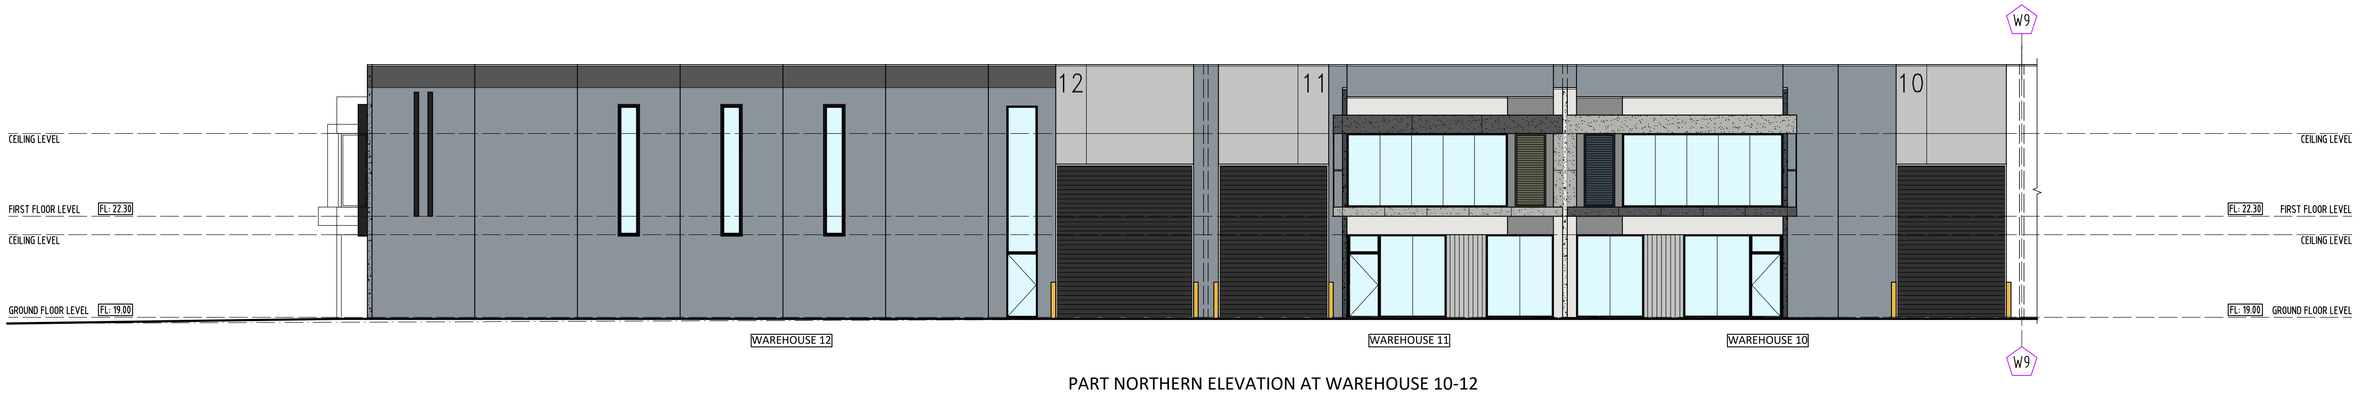


PART NORTHERN ELEVATION AT WAREHOUSE 10-12

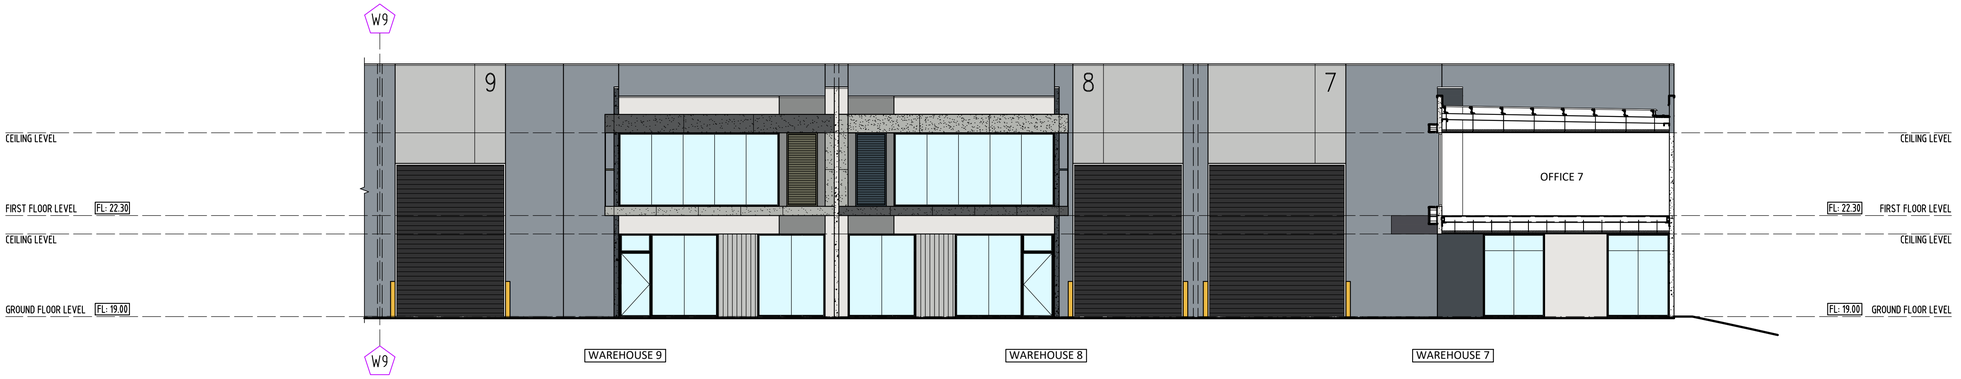

PART NORTHERN ELEVATION AT WAREHOUSE 7-9

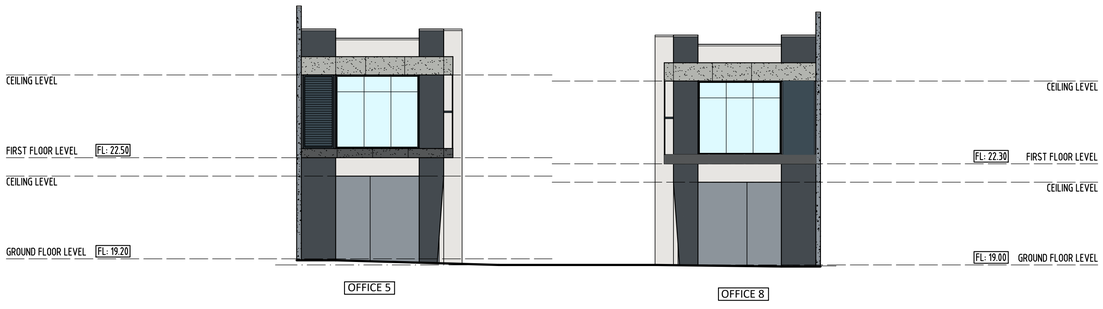

WESTERN ELEVATION AT WAREHOUSE 5 & 8

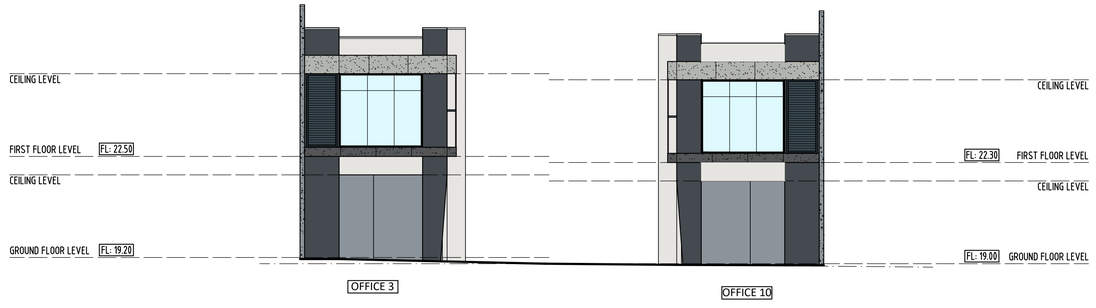

WESTERN ELEVATION AT WAREHOUSE 3 & 10

REVISIONS

THIS DRAWING AND DESIGN IS SUBJECT TO COPYRIGHT AND MAY NOT BE REPRODUCED WITHOUT PRIOR WRITTEN CONSENT FROM CREATIVE LIVING INNOVATIONS PTY LTD. CONTRACTOR TO VERIFY ALL DIMENSIONS ON SITE PRIOR TO COMMENCEMENT OF ANY WORK.
ANY DISCREPANCIES ON DRAWINGS TO BE ADVISED TO OFFICE IMMEDIATELY. FIGURED DIMENSIONS TO TAKE PRECEDENCE TO SCALED DRAWINGS.
NOTE: PLANS ARE NOT TO BE SCALED.

PRINTS A1 @ 1:100 A3 @ 1:200

PROJECT

PROPOSED WAREHOUSE AND OFFICE DEVELOPMENT
AT LOT 57, 29 AXIS BOULEVARD
OFFICER SOUTH

CLIENT

NHPB HOLDINGS PTY LTD


NORTH POINT

CREATIVE LIVING INNOVATIONS PTY LTD
SUITE 204 12-18 CORPORATE DRIVE
HEATHERTON VIC 3202
MOBILE: +61 0414 394 798
EMAIL:info@creativelivinginnovations.com.au


DATE: JULY '24
SCALE: 1:100 @ A1
SHEET: 13 OF 15
REVISION ISSUE: -
JOB No: TP 1675/25




PART SOUTHERN ELEVATION AT WAREHOUSE 10-12

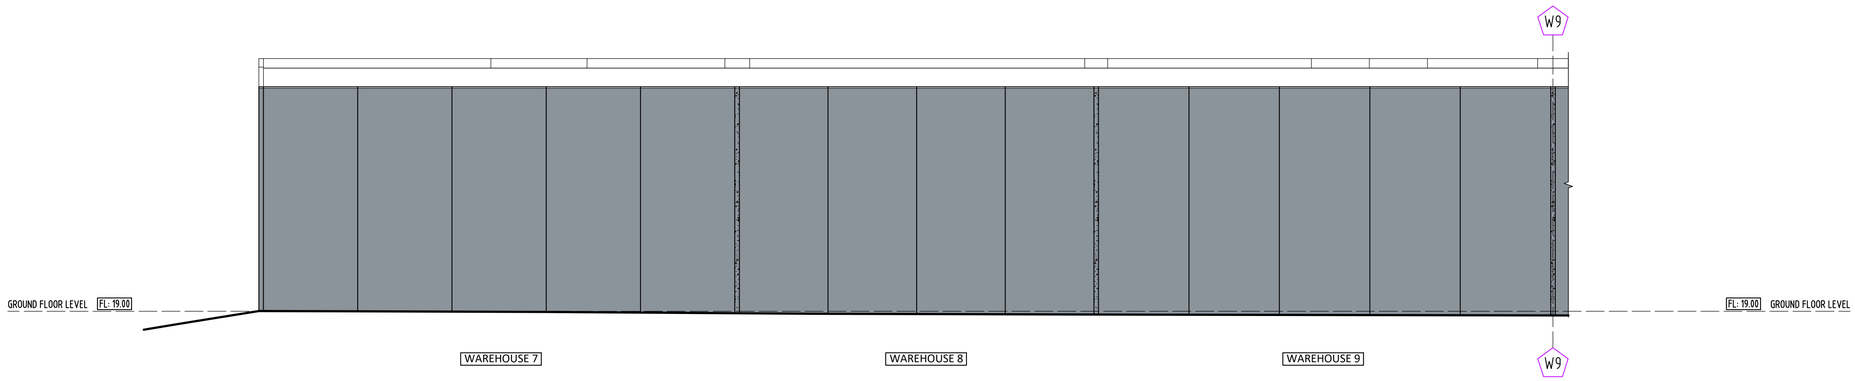

SOUTHERN ELEVATION AT WAREHOUSE 7-9

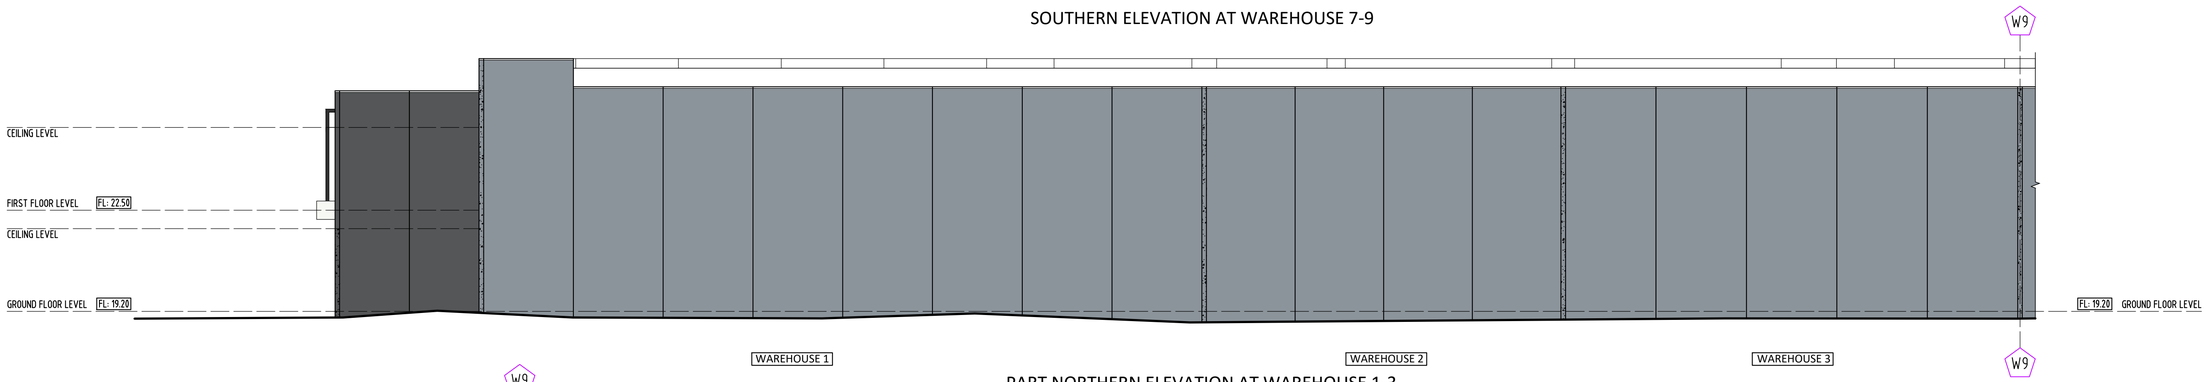

PART NORTHERN ELEVATION AT WAREHOUSE 1-3

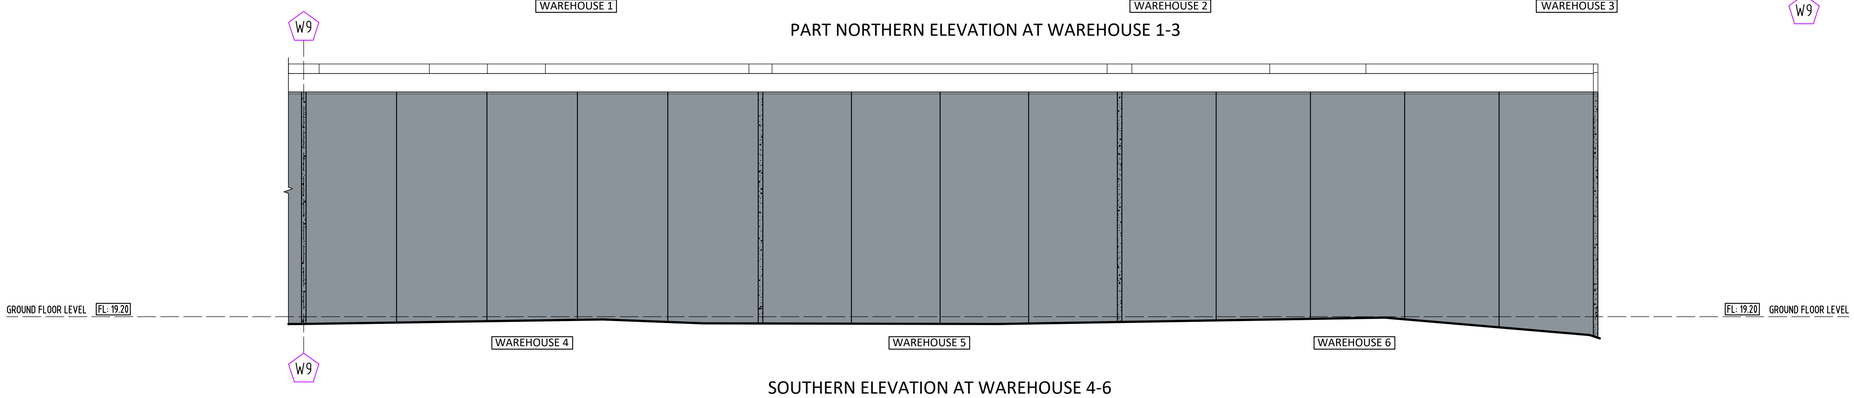

SOUTHERN ELEVATION AT WAREHOUSE 4-6

REVISIONS

THIS DRAWING AND DESIGN IS SUBJECT TO COPYRIGHT AND MAY NOT BE REPRODUCED WITHOUT PRIOR WRITTEN CONSENT FROM CREATIVE LIVING INNOVATIONS PTY LTD. CONTRACTOR TO VERIFY ALL DIMENSIONS ON SITE PRIOR TO COMMENCEMENT OF ANY WORK.
ANY DISCREPANCIES ON DRAWINGS TO BE ADVISED TO OFFICE IMMEDIATELY. FIGURED DIMENSIONS TO TAKE PRECEDENCE TO SCALED DRAWINGS.
NOTE: PLANS ARE NOT TO BE SCALED.

PRINTS A1 @ 1:100 A3 @ 1:200

PROJECT

PROPOSED WAREHOUSE AND OFFICE DEVELOPMENT
AT LOT 57, 29 AXIS BOULEVARD
OFFICER SOUTH

CLIENT

NHPB HOLDINGS PTY LTD

NORTH POINT

CREATIVE LIVING INNOVATIONS PTY LTD
SUITE 204 12-18 CORPORATE DRIVE
HEATHERTON VIC 3202
MOBILE: +61 0414 394 798
EMAIL:info@creativelivinginnovations.com.au

DATE: JULY '24

SCALE: 1:100 @ A1

SHEET: 14 OF 15

REVISION ISSUE: -

JOB No: TP 1675/25



PERSPECTIVE VIEW 1



PERSPECTIVE VIEW 2



PERSPECTIVE VIEW 3



PERSPECTIVE VIEW 4



PERSPECTIVE VIEW 5



PERSPECTIVE VIEW 6

REVISIONS

THIS DRAWING AND DESIGN IS SUBJECT TO COPYRIGHT AND MAY NOT BE REPRODUCED WITHOUT PRIOR WRITTEN CONSENT FROM CREATIVE LIVING INNOVATIONS PTY LTD. CONTRACTOR TO VERIFY ALL DIMENSIONS ON SITE PRIOR TO COMMENCEMENT OF ANY WORK.
ANY DISCREPANCIES ON DRAWINGS TO BE ADVISED TO OFFICE IMMEDIATELY. FIGURED DIMENSIONS TO TAKE PRECEDENCE TO SCALED DRAWINGS.
NOTE: PLANS ARE NOT TO BE SCALED.

PRINTS A1 @ 1:100 A3 @ 1:200

PROJECT

PROPOSED WAREHOUSE AND OFFICE DEVELOPMENT
AT LOT 57, 29 AXIS BOULEVARD
OFFICER SOUTH

CLIENT

NHPB HOLDINGS PTY LTD

NORTH POINT

CREATIVE LIVING INNOVATIONS PTY LTD
SUITE 204 12-18 CORPORATE DRIVE
HEATHERTON VIC 3202
MOBILE: +61 0414 394 798
EMAIL:info@creativelivinginnovations.com.au

DATE: JULY '24

SCALE: 1:100 @ A1

SHEET: 15 OF 15

REVISION ISSUE: -

JOB No: TP 1675/25